




[illegible]

DRAWING SHEET APPLIES TO ALL UNITS

GE Mfg. No.	Hand	Unit No.
7264807	LH	2

REVISIONS				CUSTOMER INFORMATION
REV	DESCRIPTION	DATE	BY	
0	ISSUED FOR APPROVAL	01/07/16	MAP	GE PACKAGED POWER LP, 726-9807 LMS100 60HZ EXELON PROJECT
1	REVISED PER CUSTOMER COMMENTS	02/05/16	MAP	
2	REVISED PER CUSTOMER COMMENTS	07/11/16	JG	
3	REVISED PER CUSTOMER COMMENTS	09/28/16	JG	
4	REVISED PER CUSTOMER COMMENTS	11/17/16	JG	
5	REVISED PER CUSTOMER COMMENTS	01/24/17	JG	
THIS DRAWING, DESIGN AND THE DATA CONTAINED THEREIN IS THE PROPERTY OF WILSON FIRE EQUIPMENT AND IS NOT TO BE DISTRIBUTED TO OR USED BY OTHERS WITHOUT THE EXPRESSED WRITTEN CONSENT OF WILSON FIRE EQUIPMENT.				FIRE & GAS PANEL – CAUSE AND EFFECT CHART FIRE DETECTION / CO2 SUPPRESSION SYSTEM WFE PROJECT # GE-1378
SCALE: AS SHOWN MAP DATE				
DRAWN:				
CHECKED:				
APPROVED:				

		SIZE	DRAWING NO.	REV
		B	CE-1378-01	5
		SHEET 1 OF 1		

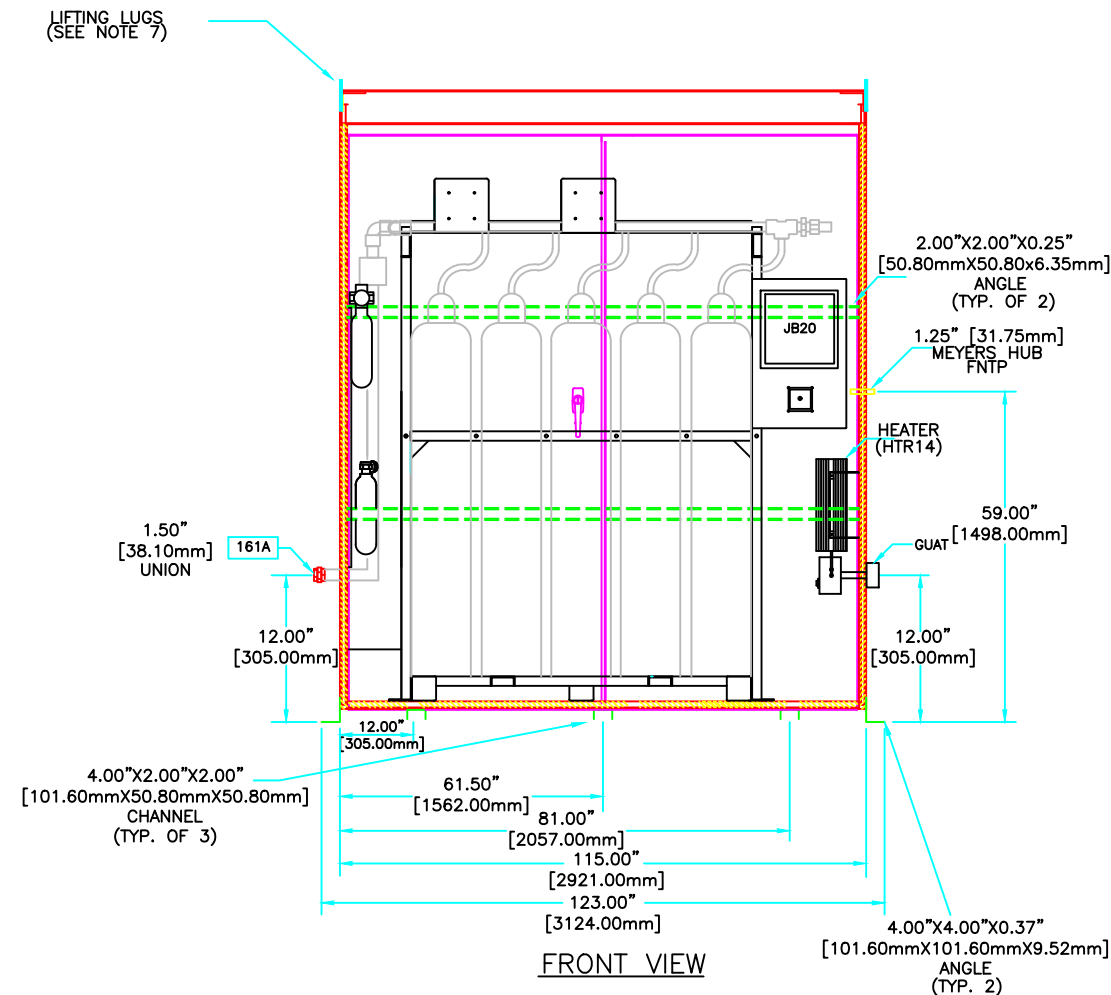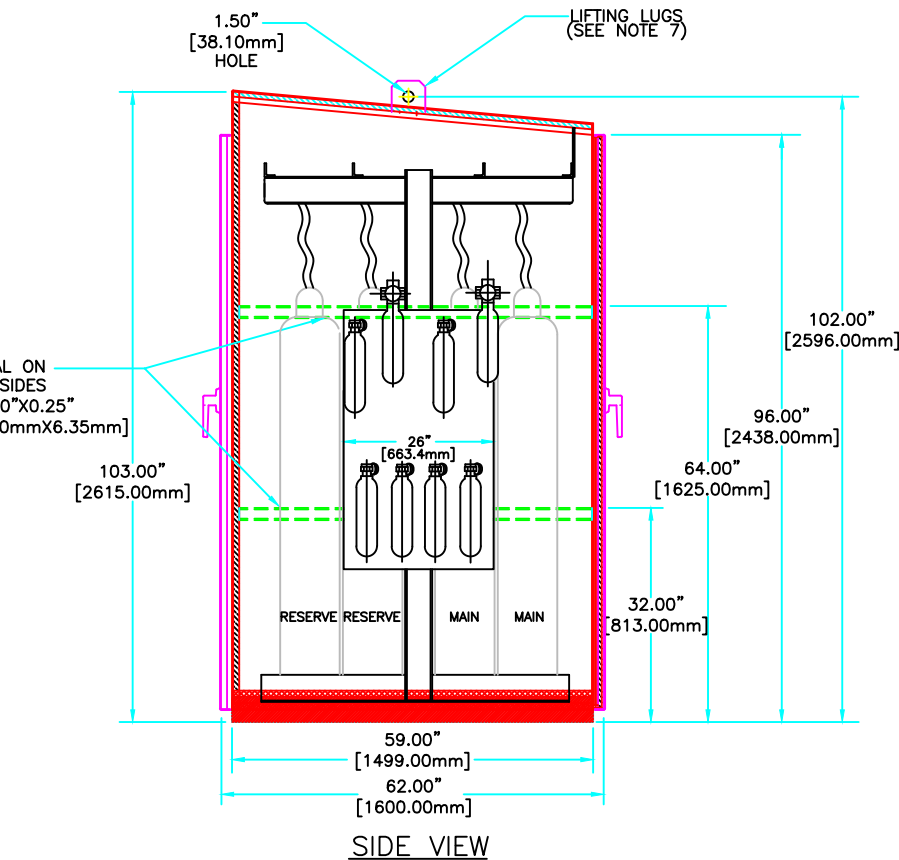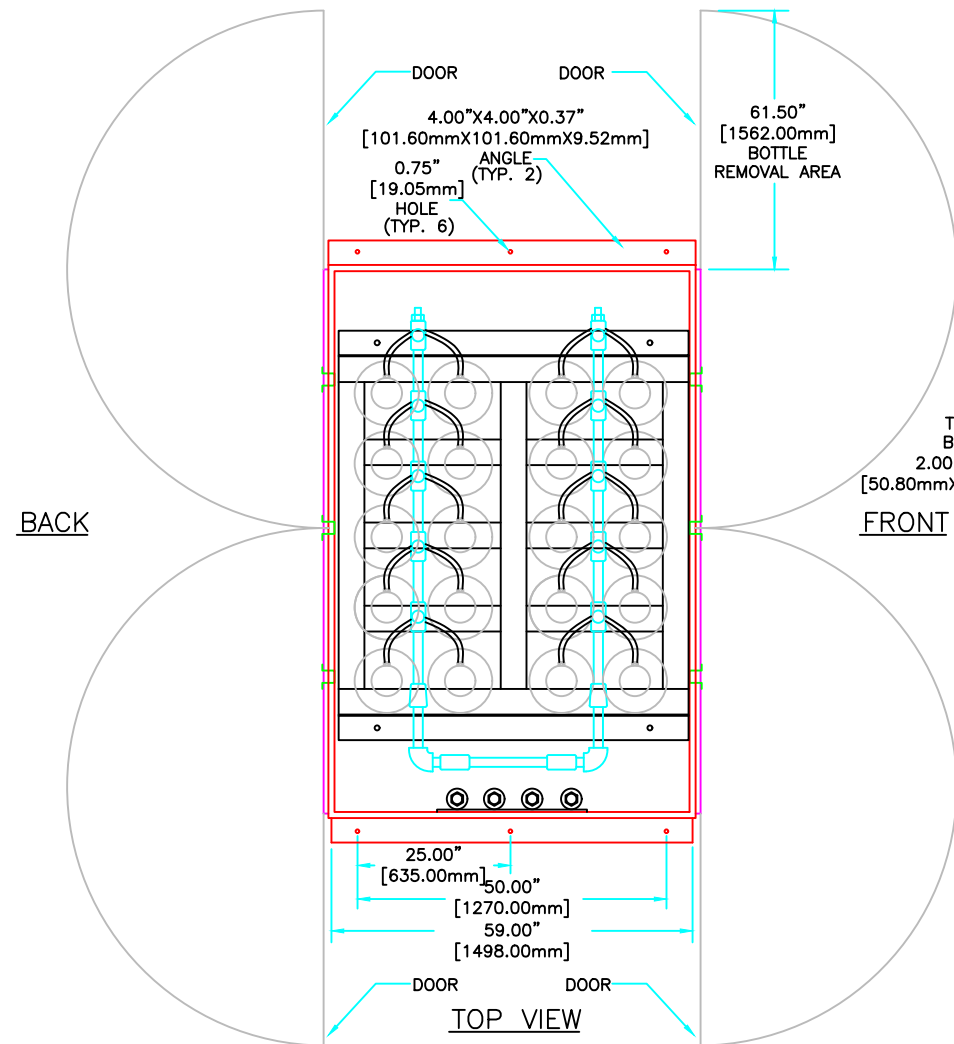

NOTES:

- CONSTRUCTION TO BE NEMA 3, FABRICATED FROM 12 GAUGE PICKLED AND OILED STEEL.
- FINISH TO BE RED POWDER COAT.
- STICK PINS ARE TO BE ARRANGED IN A 1'-0" X 1'-0" [304.80mmX304.80mm] GRID.
- ENCLOSURES WILL HAVE A 1" GRATING IN THE BOTTOM OF THE ENCLOSURE.
- COLD WEATHER ENCLOSURES WILL COME WITH CO2 RACK INSTALLED INSIDE.
- COLD WEATHER ENCLOSURES WILL COME INSULATED AND WITH A 1500 W, 208V, 1PH HEATER.
- LIFTING LUGS ARE TO BE USED FOR EMPTY ENCLOSURE ONLY, DO NOT LIFT WITH CYLINDERS INSIDE ENCLOSURE.
- TOLERANCE ON FLANGE CONNECTIONS $\pm 0.12"$ [3.04mm].
- DIMENSIONS AND VALUES IN [] ARE SI UNITS AND ARE GIVEN FOR REFERENCE ONLY. EQUIPMENT WILL BE DESIGNED AND MANUFACTURED USING ENGLISH UNITS ONLY.
- 2.00"x2.00"x0.25" [51mmX51mmX6mm] ANGLES IS TYPICAL ON BACK OF PANEL.
- TOLERANCES:
LINEAR DIMENSION $\pm 0.12"$ [3.04mm].
ANGULAR ± 0.5

ENCLOSURE WEIGHT - 1900 lbs. [861.82kg]
ENCLOSURE WEIGHT W/ BOTTLES
AND RACK ASSEMBLY - 8800 lbs. [3991.61kg]

DRAWING SHEET APPLIES TO ALL UNITS


GE Mfg. No.	Hand	Unit No.
7264807	LH	2

REVISIONS				THIS DRAWING, DESIGN AND THE DATA CONTAINED THEREIN IS THE PROPERTY OF WILSON FIRE EQUIPMENT AND IS NOT TO BE DISTRIBUTED TO OR USED BY OTHERS WITHOUT THE EXPRESSED WRITTEN CONSENT OF WILSON FIRE EQUIPMENT.	
REV	DESCRIPTION	DATE	BY		
0	ISSUED FOR APPROVAL	01/07/16	MAP	SCALE:	AS SHOWN
1	REVISED PER CUSTOMER COMMENTS	02/05/16	MAP	DRAWN:	MAP 01/07/16
2	REVISED PER CUSTOMER COMMENTS	07/11/16	JG	CHECKED:	LMW 01/24/17
3	REVISED PER CUSTOMER COMMENTS	09/28/16	JG	APPROVED:	LMW 01/24/17
4	REVISED PER CUSTOMER COMMENTS	11/17/16	JG		
5	REVISED PER CUSTOMER COMMENTS	01/24/17	JG		

WILSON FIRE EQUIPMENT & SERVICE CO.	
7303 EMPIRE CENTRAL DRIVE HOUSTON, TEXAS 77040 (713) 896-4747	
CUSTOMER INFORMATION	
GE PACKAGED POWER LP. 7264807	
LMS100 EXELON PROJECT 20 BOTTLE COLD WEATHER ENCLOSURE GENERAL ARRANGEMENT - CO2 SKID CO2 FIRE PROTECTION SYSTEM WFE PROJECT # GE-1378	



SIZE	DRAWING NO.	REV
B	GA-1378-1 SHEET 1 OF 8	5

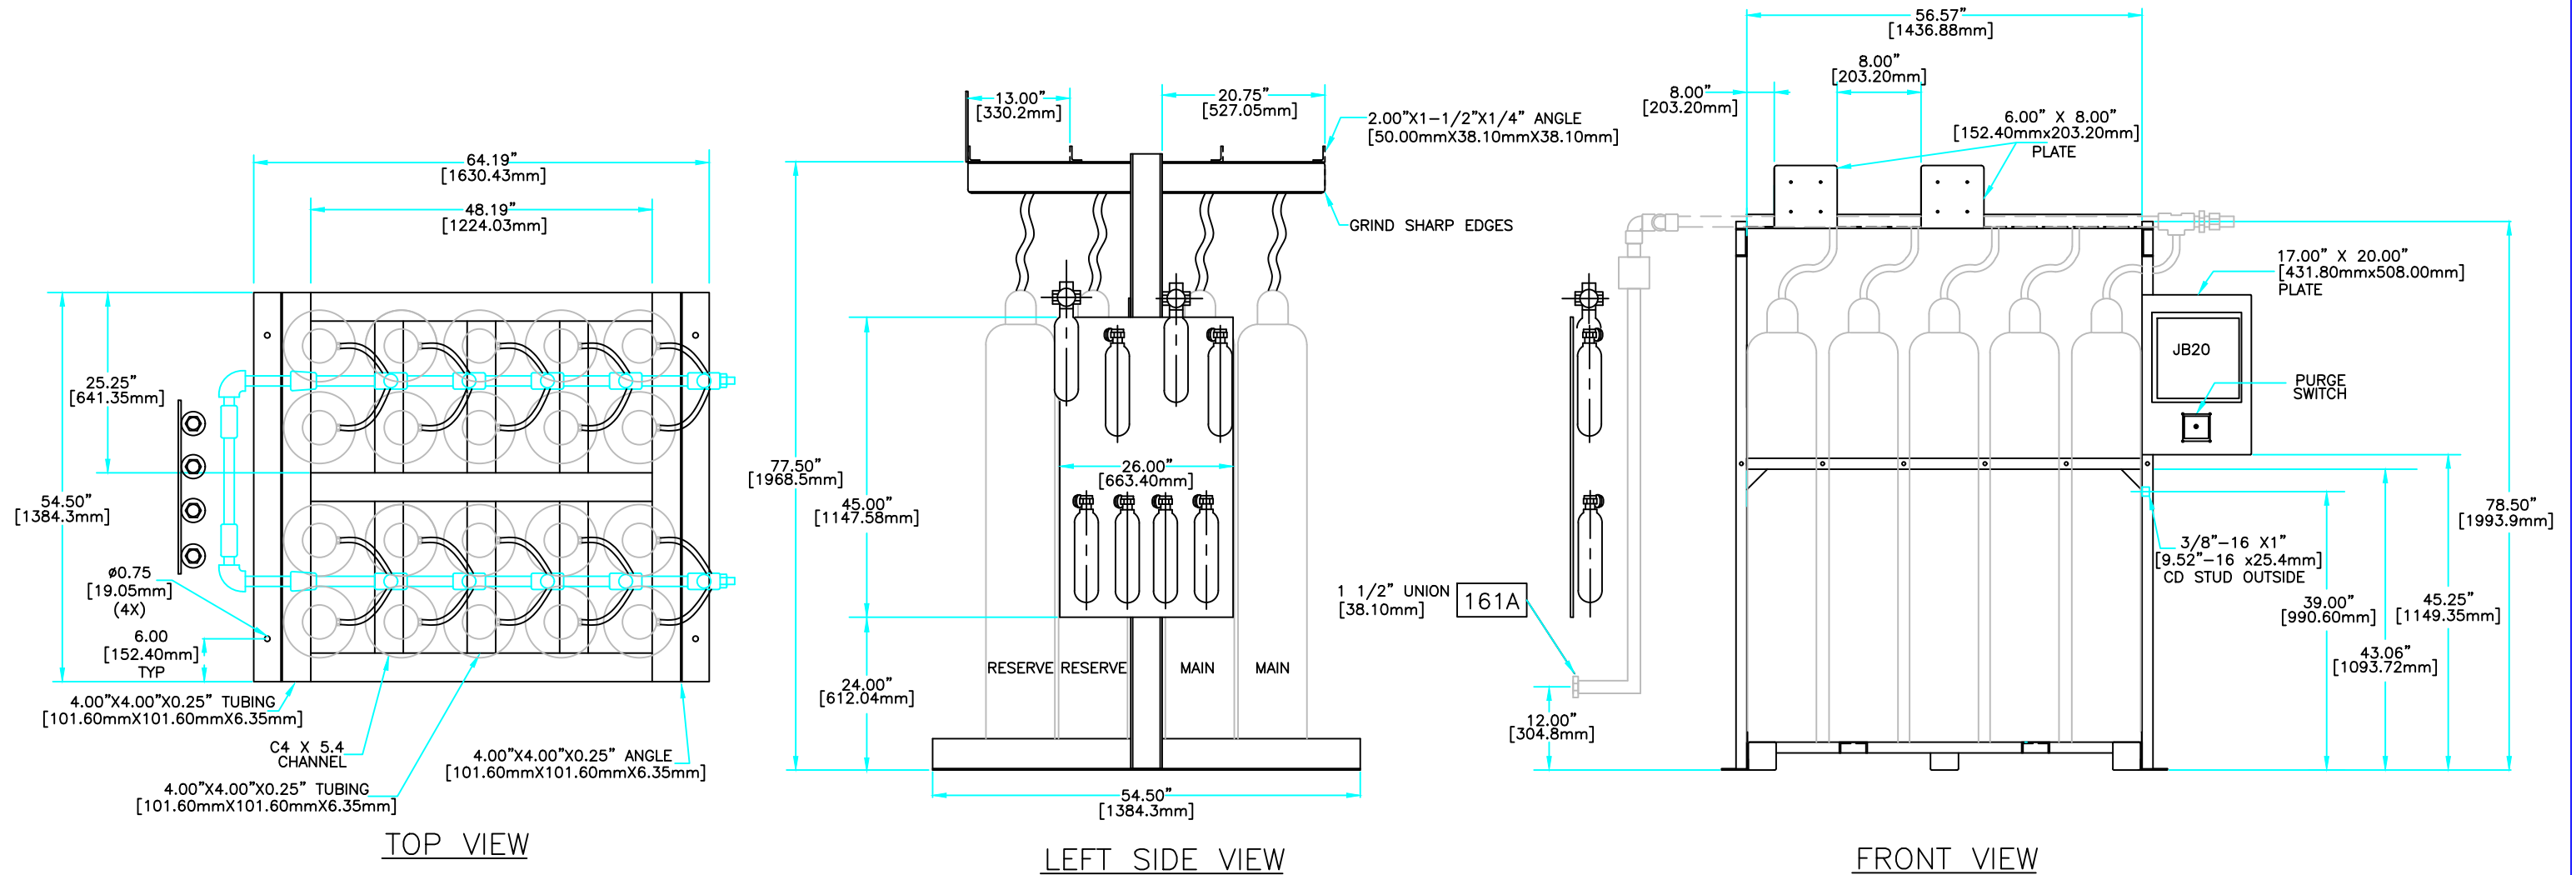

CONNECTION LEGEND:

161A FIRE PROTECTION – CO2, BOTTLE SKID, OUTLET TO MAIN UNIT 1.50\"[38.10mm] NPT 3000#

NOTES:

- WEIGHT OF SKID = 900 LBS. [408.23kg]
20 BOTTLES @ 300 LBS. [136.07kg] EA. = 6000 LBS. [2721.55kg]
TOTAL WEIGHT = 6900 LBS. [3129.78kg]
- RED POWDER COAT FINISH.
- DIMENSIONS AND VALUES IN [] ARE SI UNITS AND ARE GIVEN FOR REFERENCE ONLY. EQUIPMENT WILL BE DESIGNED AND MANUFACTURED USING ENGLISH UNITS ONLY. DIMENSIONS ARE IN INCHES.
- TOLERANCES:
FLANGE CONNECTION ± 0.12 \"[3.17mm]
LINEAR DIMENSION ± 0.12 \"[3.17mm]
ANGULAR ± 0.5
- RADIUS CORNERS (8) TYPICAL.



DRAWING SHEET APPLIES TO ALL UNITS

GE Mfg. No.	Hand	Unit No.
7264807	LH	2

REVISIONS				THIS DRAWING, DESIGN AND THE DATA CONTAINED THEREIN IS THE PROPERTY OF WILSON FIRE EQUIPMENT AND IS NOT TO BE DISTRIBUTED TO OR USED BY OTHERS WITHOUT THE EXPRESSED WRITTEN CONSENT OF WILSON FIRE EQUIPMENT. SCALE: N.T.S DATE DRAWN: MAP 01/07/16 CHECKED: LMW 01/24/17 APPROVED: LMW 01/24/17	
REV	DESCRIPTION	DATE	BY		
0	ISSUED FOR APPROVAL	01/07/16	MAP		
1	REVISED PER CUSTOMER COMMENTS	02/05/16	MAP		
2	REVISED PER CUSTOMER COMMENTS	07/11/16	JG		
3	REVISED PER CUSTOMER COMMENTS	09/28/16	JG		
4	REVISED PER CUSTOMER COMMENTS	11/17/16	JG		
5	REVISED PER CUSTOMER COMMENTS	01/24/17	JG		

WILSON FIRE EQUIPMENT & SERVICE CO. 7303 EMPIRE CENTRAL DRIVE HOUSTON, TEXAS 77040 (713) 896-4747	
CUSTOMER INFORMATION GE PACKAGED POWER LP. 7264807	
LMS100 EXELON PROJECT 20 BOTTLES NO SUNSHIELD GENERAL ARRANGEMENT CO2 FIRE PROTECTION SYSTEM WFE PROJECT # GE-1378	

		
SIZE	DRAWING NO.	REV
B	GA-1378-2 SHEET 2 OF 8	5

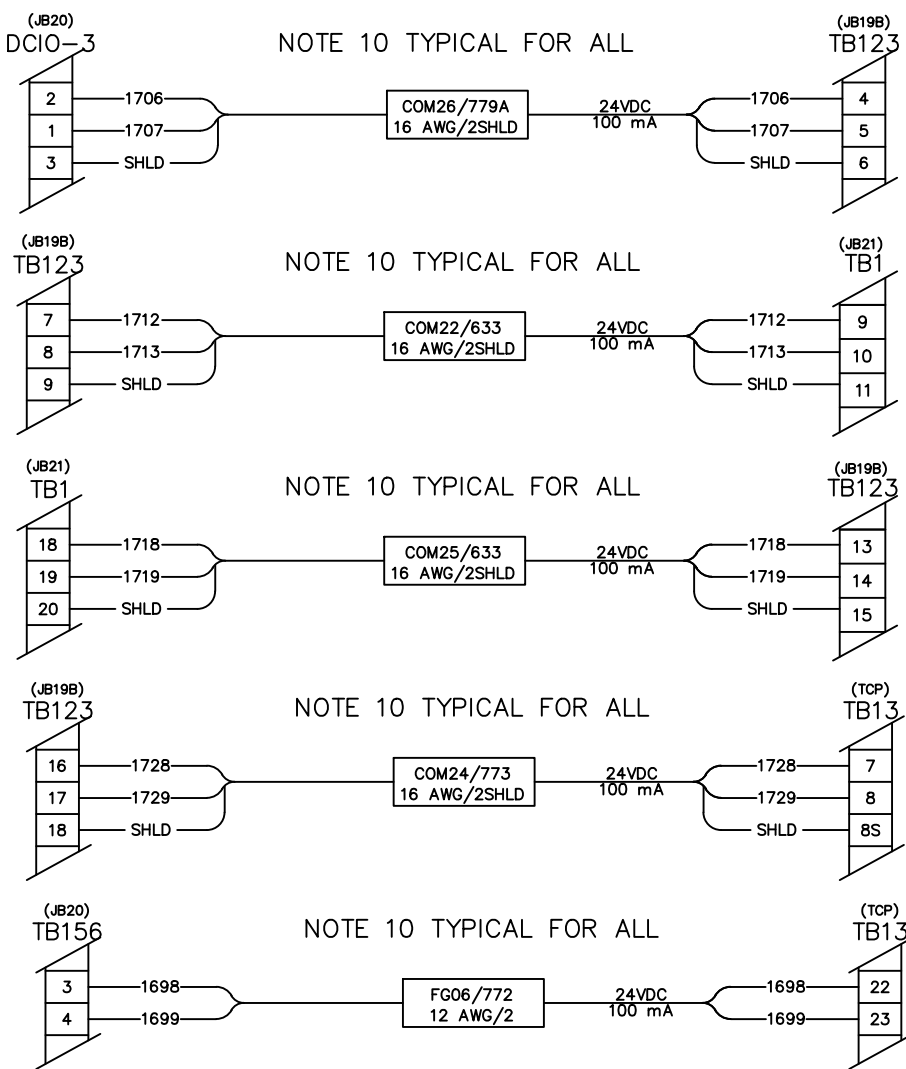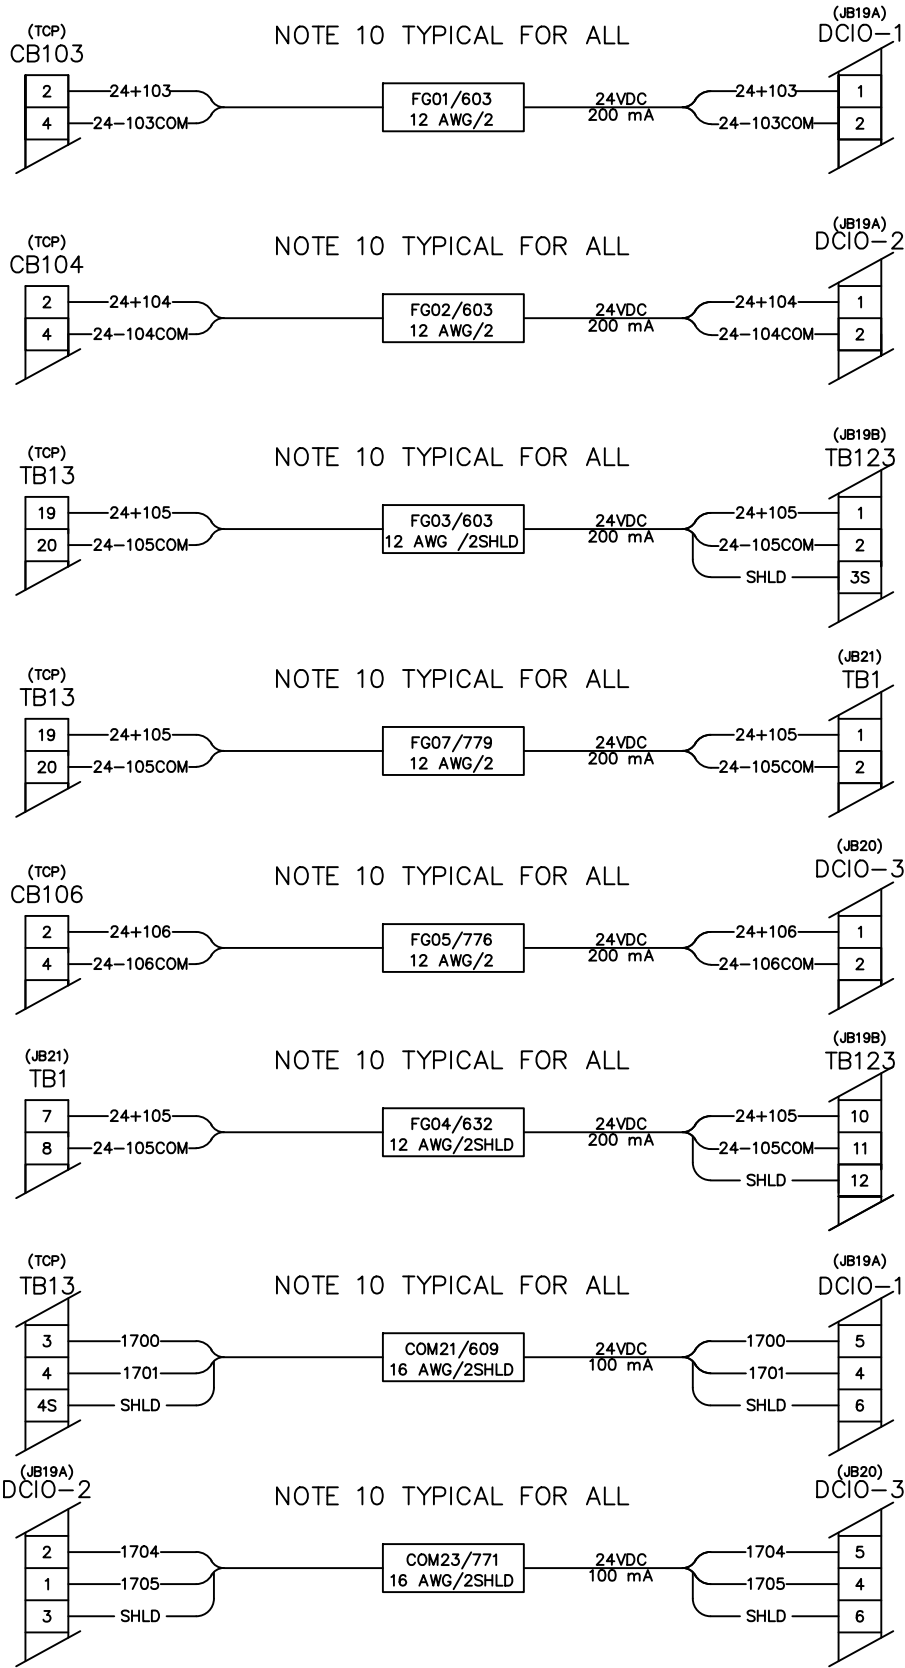

- NOTES:
- 1___ WIRES, MATERIALS, AND CONSTRUCTION SHALL CONFORM TO ALL RELEVANT NORTH AMERICAN STANDARDS
- 2___ JUMPER MUST BE INSTALLED FOR PROPER OPERATION.
USE 16 AWG WIRE
- 3___ WIRE SIZED FOR 100 METERS IN LENGTH
- 4___ USE 16 AWG 28.86 PF/m TWISTED PAIR SHIELDED CABLE OR EQUAL. KEEP CABLE LENGTH TO 100m OR LESS FOR PROPER OPERATION.
- 5___ INSURE JUNCTION WIRES ARE 14 AWG (BY OTHERS)
- 6___ 14 AWG JUMPER WIRE (BY OTHERS)
- 7___ CABLE CANNOT BE MORE THAN 100 METERS LONG. OTHER MEANS MUST BE USED IF A GREATER DISTANCE IS REQUIRED. (BY OTHERS)
- 8___ SHIELDED PAIR USED ON PLC TERMINALS 15 THRU 23 OVER ALL SHIELD ON PLC TERMINAL 34. (BY OTHERS)
- 9___ SHIELDED PAIR USED ON PLC TERMINALS 45 THRU 59 OVER ALL SHIELD ON PLC TERMINAL 60. (BY OTHERS)
- 10___ FIRE PROTECTION CABLES SHOULD BE SEGREGATED AS FAR AS POSSIBLE FROM OTHER CABLES. (BY OTHERS)
- 11___ ALL SHIELDING WILL HAVE A MAXIMUM 2in. (50.8mm) EXPOSED UNSHIELDED LENGTH OF WIRE AT TERMINAL END. (BY OTHERS)
- 12___ THE CUSTOMER IS ADVISED TO MAKE ALLOWANCES FOR CABLE LENGTHS GREATER THAN 330 FEET (100 METERS) SO AS TO LIMIT THE VOLTAGE DROPS TO A 3% MAXIMUM. (BY OTHERS)
- 13___ IDENTIFIES CONDUCTORS THAT SHALL BE ROUTED WITH SEGREGATION FROM ALL OTHER CONDUCTORS CONFORMS TO IEC STANDARD EN60204-1, SEGREGATION SHALL BE MAINTAINED WITH BARRIER, OR >2 INCHES[51mm] WITHOUT BARRIER WHERE POSSIBLE. (BY OTHERS)
- 14___ ALL (PE) PROTECTIVE EARTH WIRES WILL BE GRN/YEL IN COLOR. (BY OTHERS)

WIRE GAUGE CONVERSION TABLE
(AMERICAN WIRE GAUGE-METRIC)

US Standard AWG	NEAREST AVAILABLE CROSS-SECTION mm ²
22	0.5
18	0.75
16	1.5
14	2.5
12	4.0
10	6.0
8	10.0
6	16.0
4	25.0
2	35.0


DRAWING SHEET APPLIES TO ALL UNITS

GE Mfg. No.	Hand	Unit No.
7264807	LH	2

REVISIONS				THIS DRAWING, DESIGN AND THE DATA CONTAINED THEREIN IS THE PROPERTY OF WILSON FIRE EQUIPMENT AND IS NOT TO BE DISTRIBUTED TO OR USED BY OTHERS WITHOUT THE EXPRESSED WRITTEN CONSENT OF WILSON FIRE EQUIPMENT.
REV	DESCRIPTION	DATE	BY	
0	ISSUED FOR APPROVAL	01/07/16	MAP	
1	REVISED PER CUSTOMER COMMENTS	02/05/16	MAP	
2	REVISED PER CUSTOMER COMMENTS	07/11/16	MAP	
3	REVISED PER CUSTOMER COMMENTS	09/28/16	JG	
4	REVISED PER CUSTOMER COMMENTS	11/17/16	JG	
5	REVISED PER CUSTOMER COMMENTS	01/24/17	JG	
SCALE: AS SHOWN				DATE
DRAWN: MAP				01/07/16
CHECKED: LMW				01/24/17
APPROVED: LMW				01/24/17

WILSON FIRE EQUIPMENT & SERVICE CO. 7303 EMPIRE CENTRAL DRIVE HOUSTON, TEXAS 77040 (713) 896-4747	
CUSTOMER INFORMATION	
GE PACKAGE POWER LP. 7264807	
LMS100 60HZ EXELON PROJECT	
CUSTOMER INTERCONNECT WIRING FIRE AND GAS PROTECTION WFE PROJECT # GE-1378	

		
SIZE	DRAWING NO.	REV
B	IW-1378-01 SHEET 1 OF 1	5

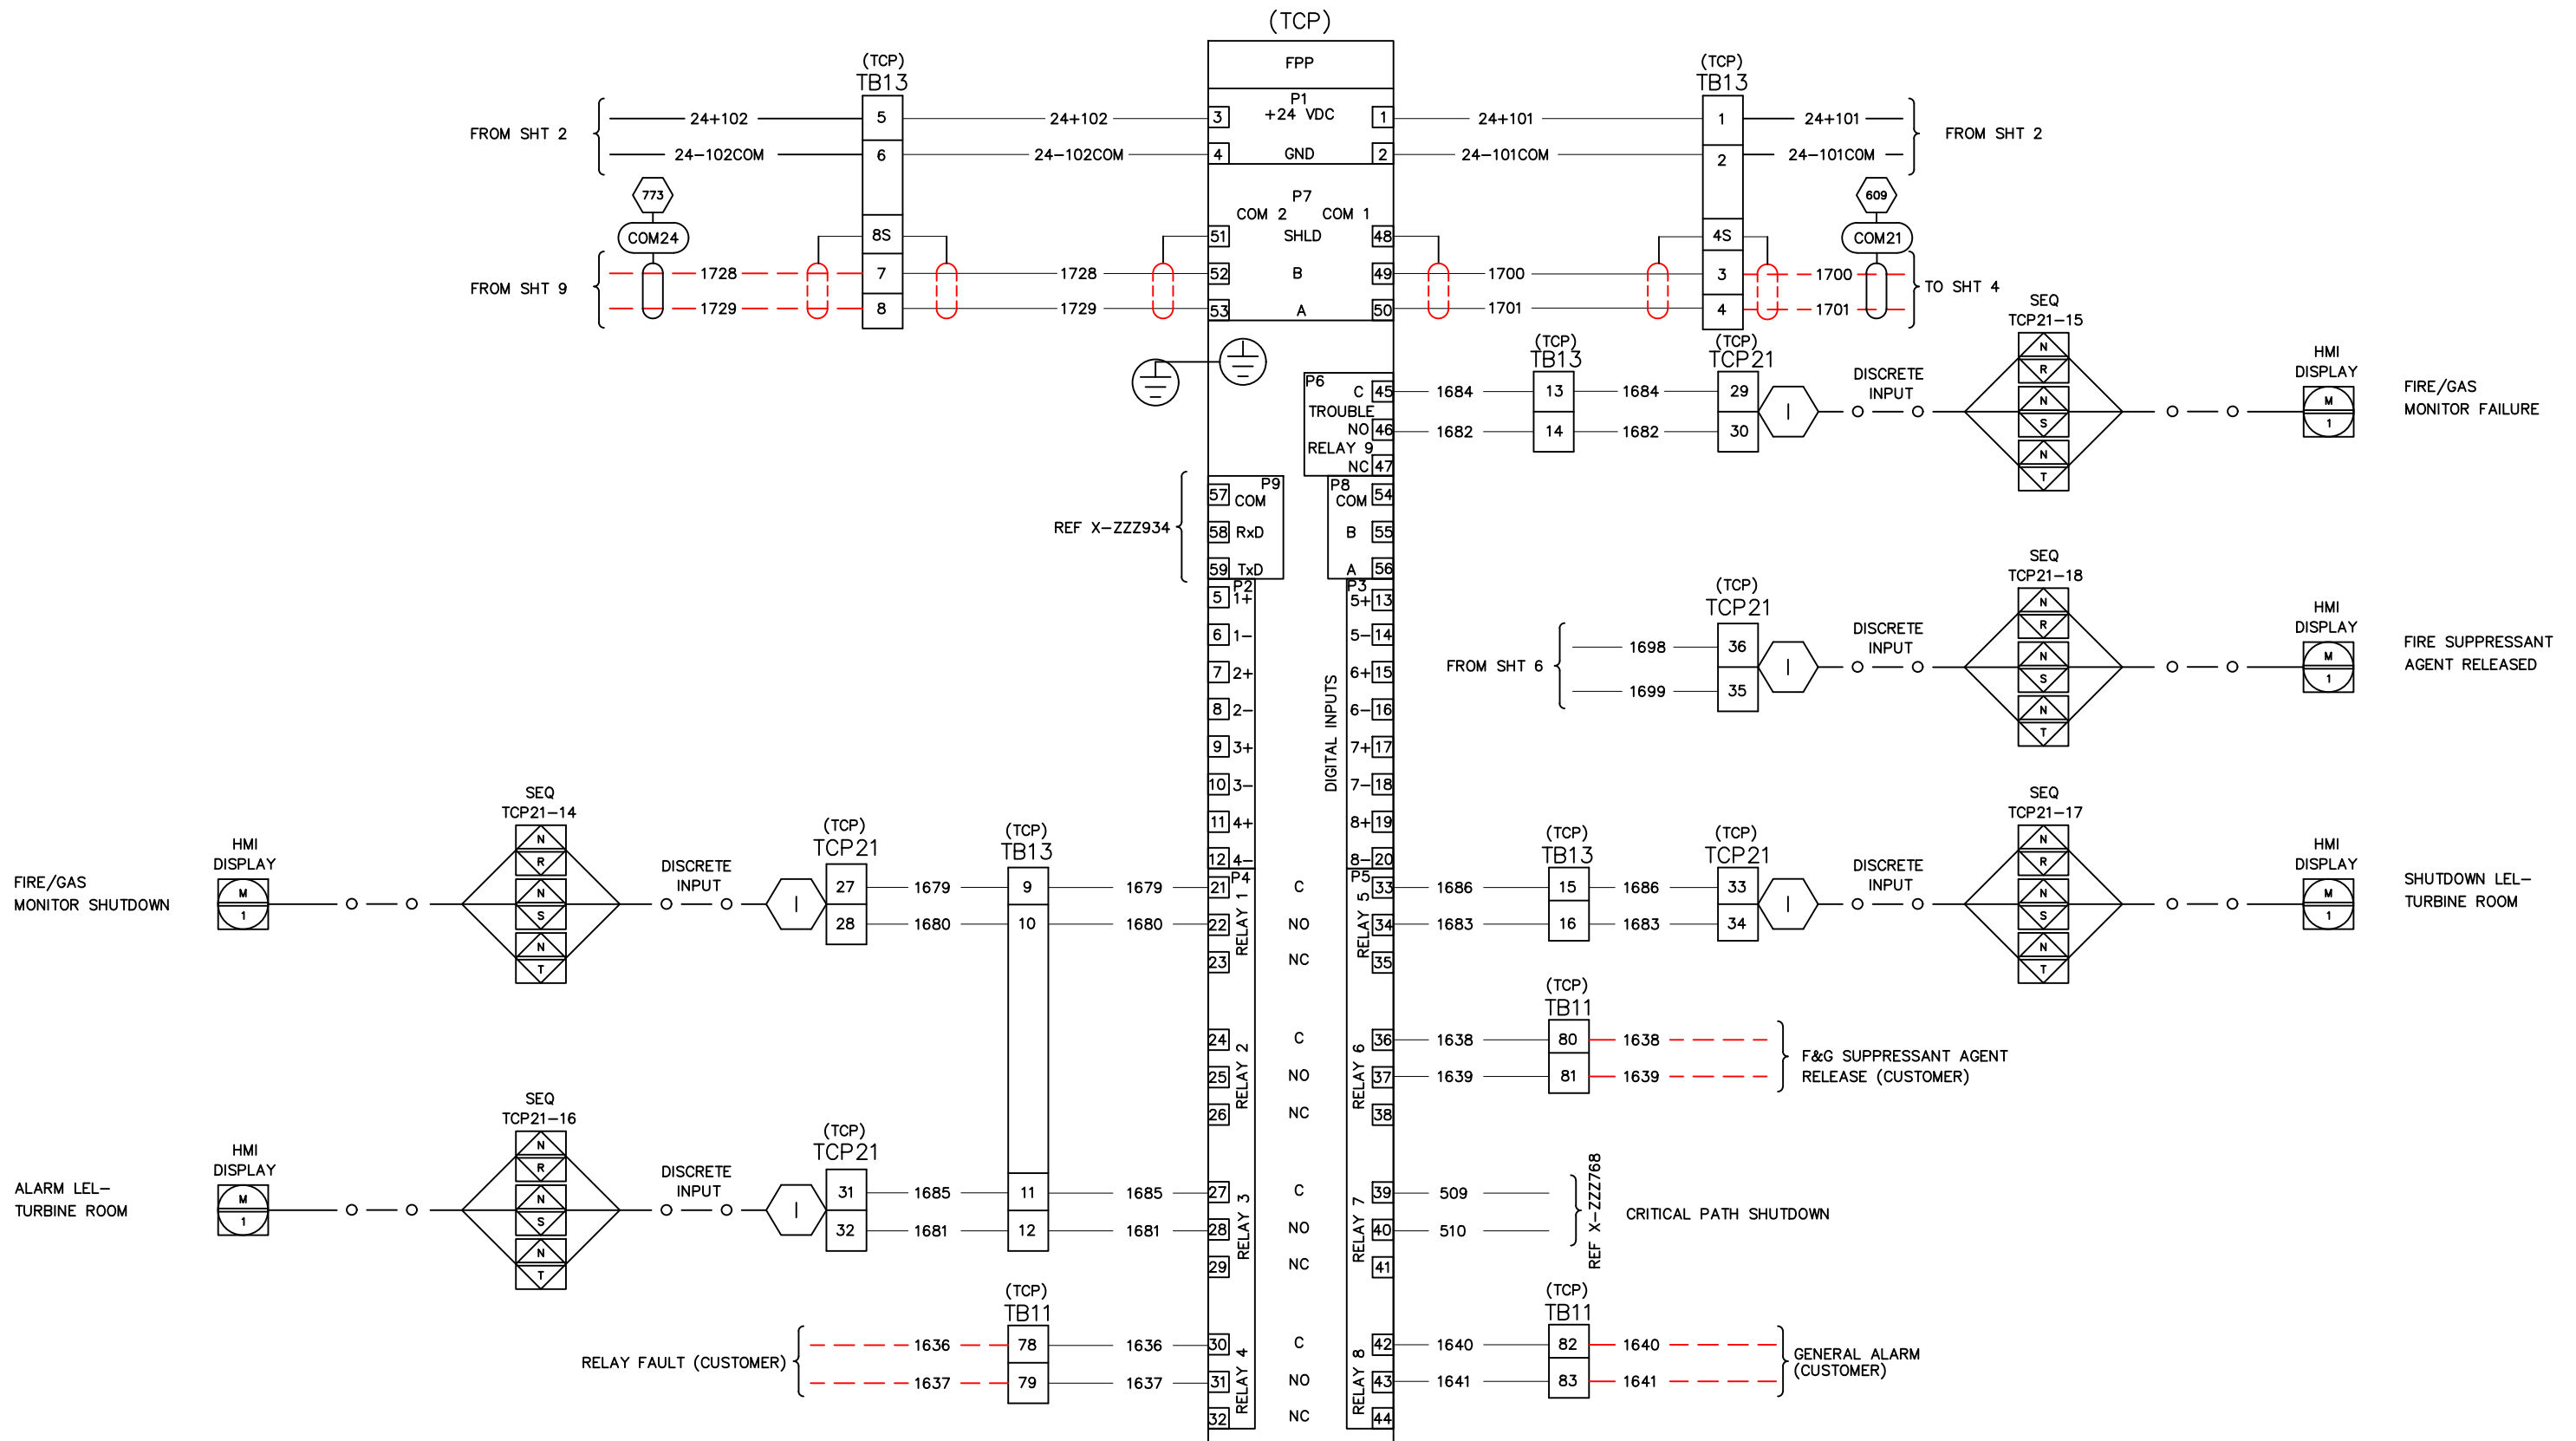

DRAWING SHEET APPLIES TO ALL UNITS

GE Mfg. No.	Hand	Unit No.
7264807	LH	2

REVISIONS			
REV	DESCRIPTION	DATE	BY
0	ISSUED FOR APPROVAL	01/07/16	MAP
1	REVISED PER CUSTOMER COMMENTS	02/05/16	MAP
2	REVISED PER CUSTOMER COMMENTS	07/11/16	JG
3	REVISED PER CUSTOMER COMMENTS	09/28/16	JG
4	REVISED PER CUSTOMER COMMENTS	11/17/16	JG
5	REVISED PER CUSTOMER COMMENTS	01/24/17	JG

THIS DRAWING, DESIGN AND THE DATA CONTAINED THEREIN IS THE PROPERTY OF WILSON FIRE EQUIPMENT AND IS NOT TO BE DISTRIBUTED TO OR USED BY OTHERS WITHOUT THE EXPRESSED WRITTEN CONSENT OF WILSON FIRE EQUIPMENT.

SCALE:	AS SHOWN	DATE
DRAWN:	MAP	01/07/16
CHECKED:	LMW	01/24/17
APPROVED:	LMW	01/24/17

WILSON FIRE EQUIPMENT & SERVICE CO.
7303 EMPIRE CENTRAL DRIVE HOUSTON, TEXAS 77040 (713) 896-4747

CUSTOMER INFORMATION


GE PACKAGED POWER LP. 7264807

LMS100 60HZ
EXELON PROJECT

SYSTEM WIRING - CONTROL PANEL
FIRE DETECTION / CO2 SUPPRESSION SYSTEM
WFE PROJECT # GE-1378



SIZE	DRAWING NO.	REV
B	SW-1378-03 SHEET 3 OF 15	5

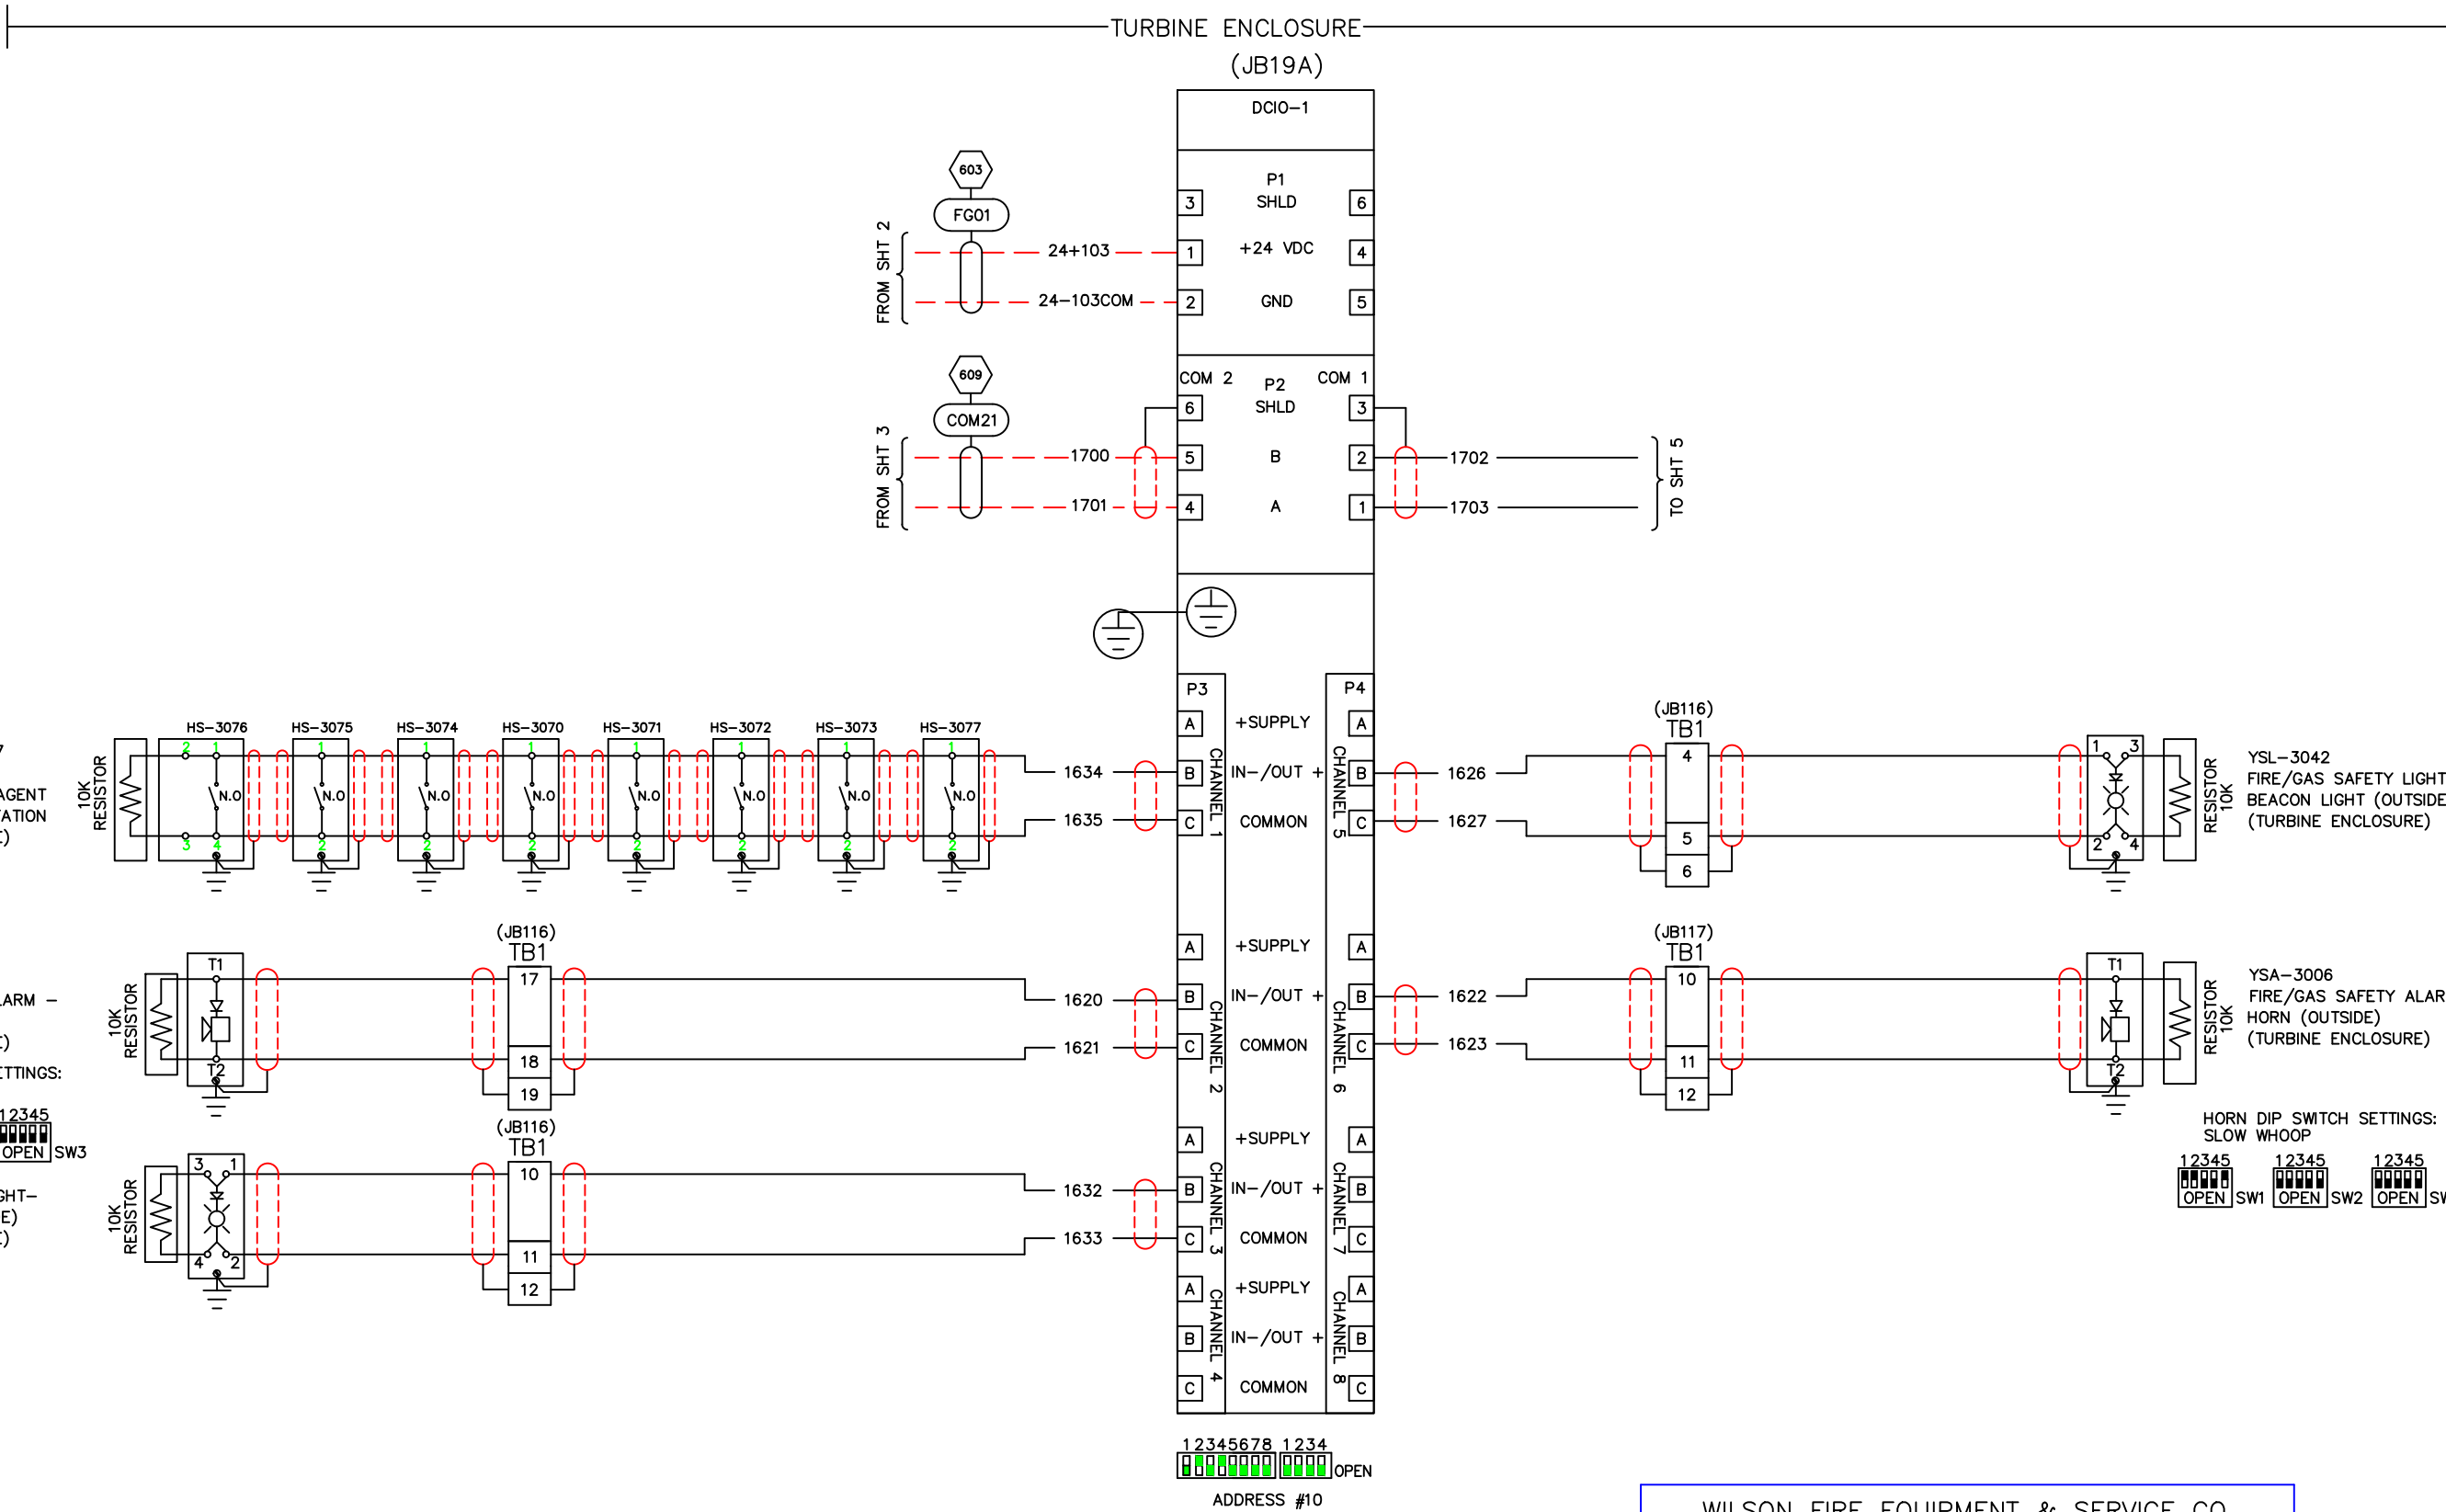

DRAWING SHEET APPLIES TO ALL UNITS

GE Mfg. No.	Hand	Unit No.
7264807	LH	2

REVISIONS			
REV	DESCRIPTION	DATE	BY
0	ISSUED FOR APPROVAL	01/07/16	MAP
1	REVISED PER CUSTOMER COMMENTS	02/05/16	MAP
2	REVISED PER CUSTOMER COMMENTS	07/11/16	JG
3	REVISED PER CUSTOMER COMMENTS	09/28/16	JG
4	REVISED PER CUSTOMER COMMENTS	11/17/16	JG
5	REVISED PER CUSTOMER COMMENTS	01/24/17	JG


THIS DRAWING, DESIGN AND THE DATA CONTAINED THEREIN IS THE PROPERTY OF WILSON FIRE EQUIPMENT AND IS NOT TO BE DISTRIBUTED TO OR USED BY OTHERS WITHOUT THE EXPRESSED WRITTEN CONSENT OF WILSON FIRE EQUIPMENT.

SCALE:	AS SHOWN	DATE
DRAWN:	MAP	01/07/16
CHECKED:	LMW	01/24/17
APPROVED:	LMW	01/24/17

WILSON FIRE EQUIPMENT & SERVICE CO. 7303 EMPIRE CENTRAL DRIVE HOUSTON, TEXAS 77040 (713) 896-4747	
CUSTOMER INFORMATION	
GE PACKAGED POWER LP. 7264807	
LMS100 60HZ EXELON PROJECT	
SYSTEM WIRING - DCIO-1 FIRE DETECTION / CO2 SUPPRESSION SYSTEM WFE PROJECT # GE-1378	

		
SIZE	DRAWING NO.	REV
B	SW-1378-04 SHEET 4 OF 15	5

TURBINE ENCLOSURE

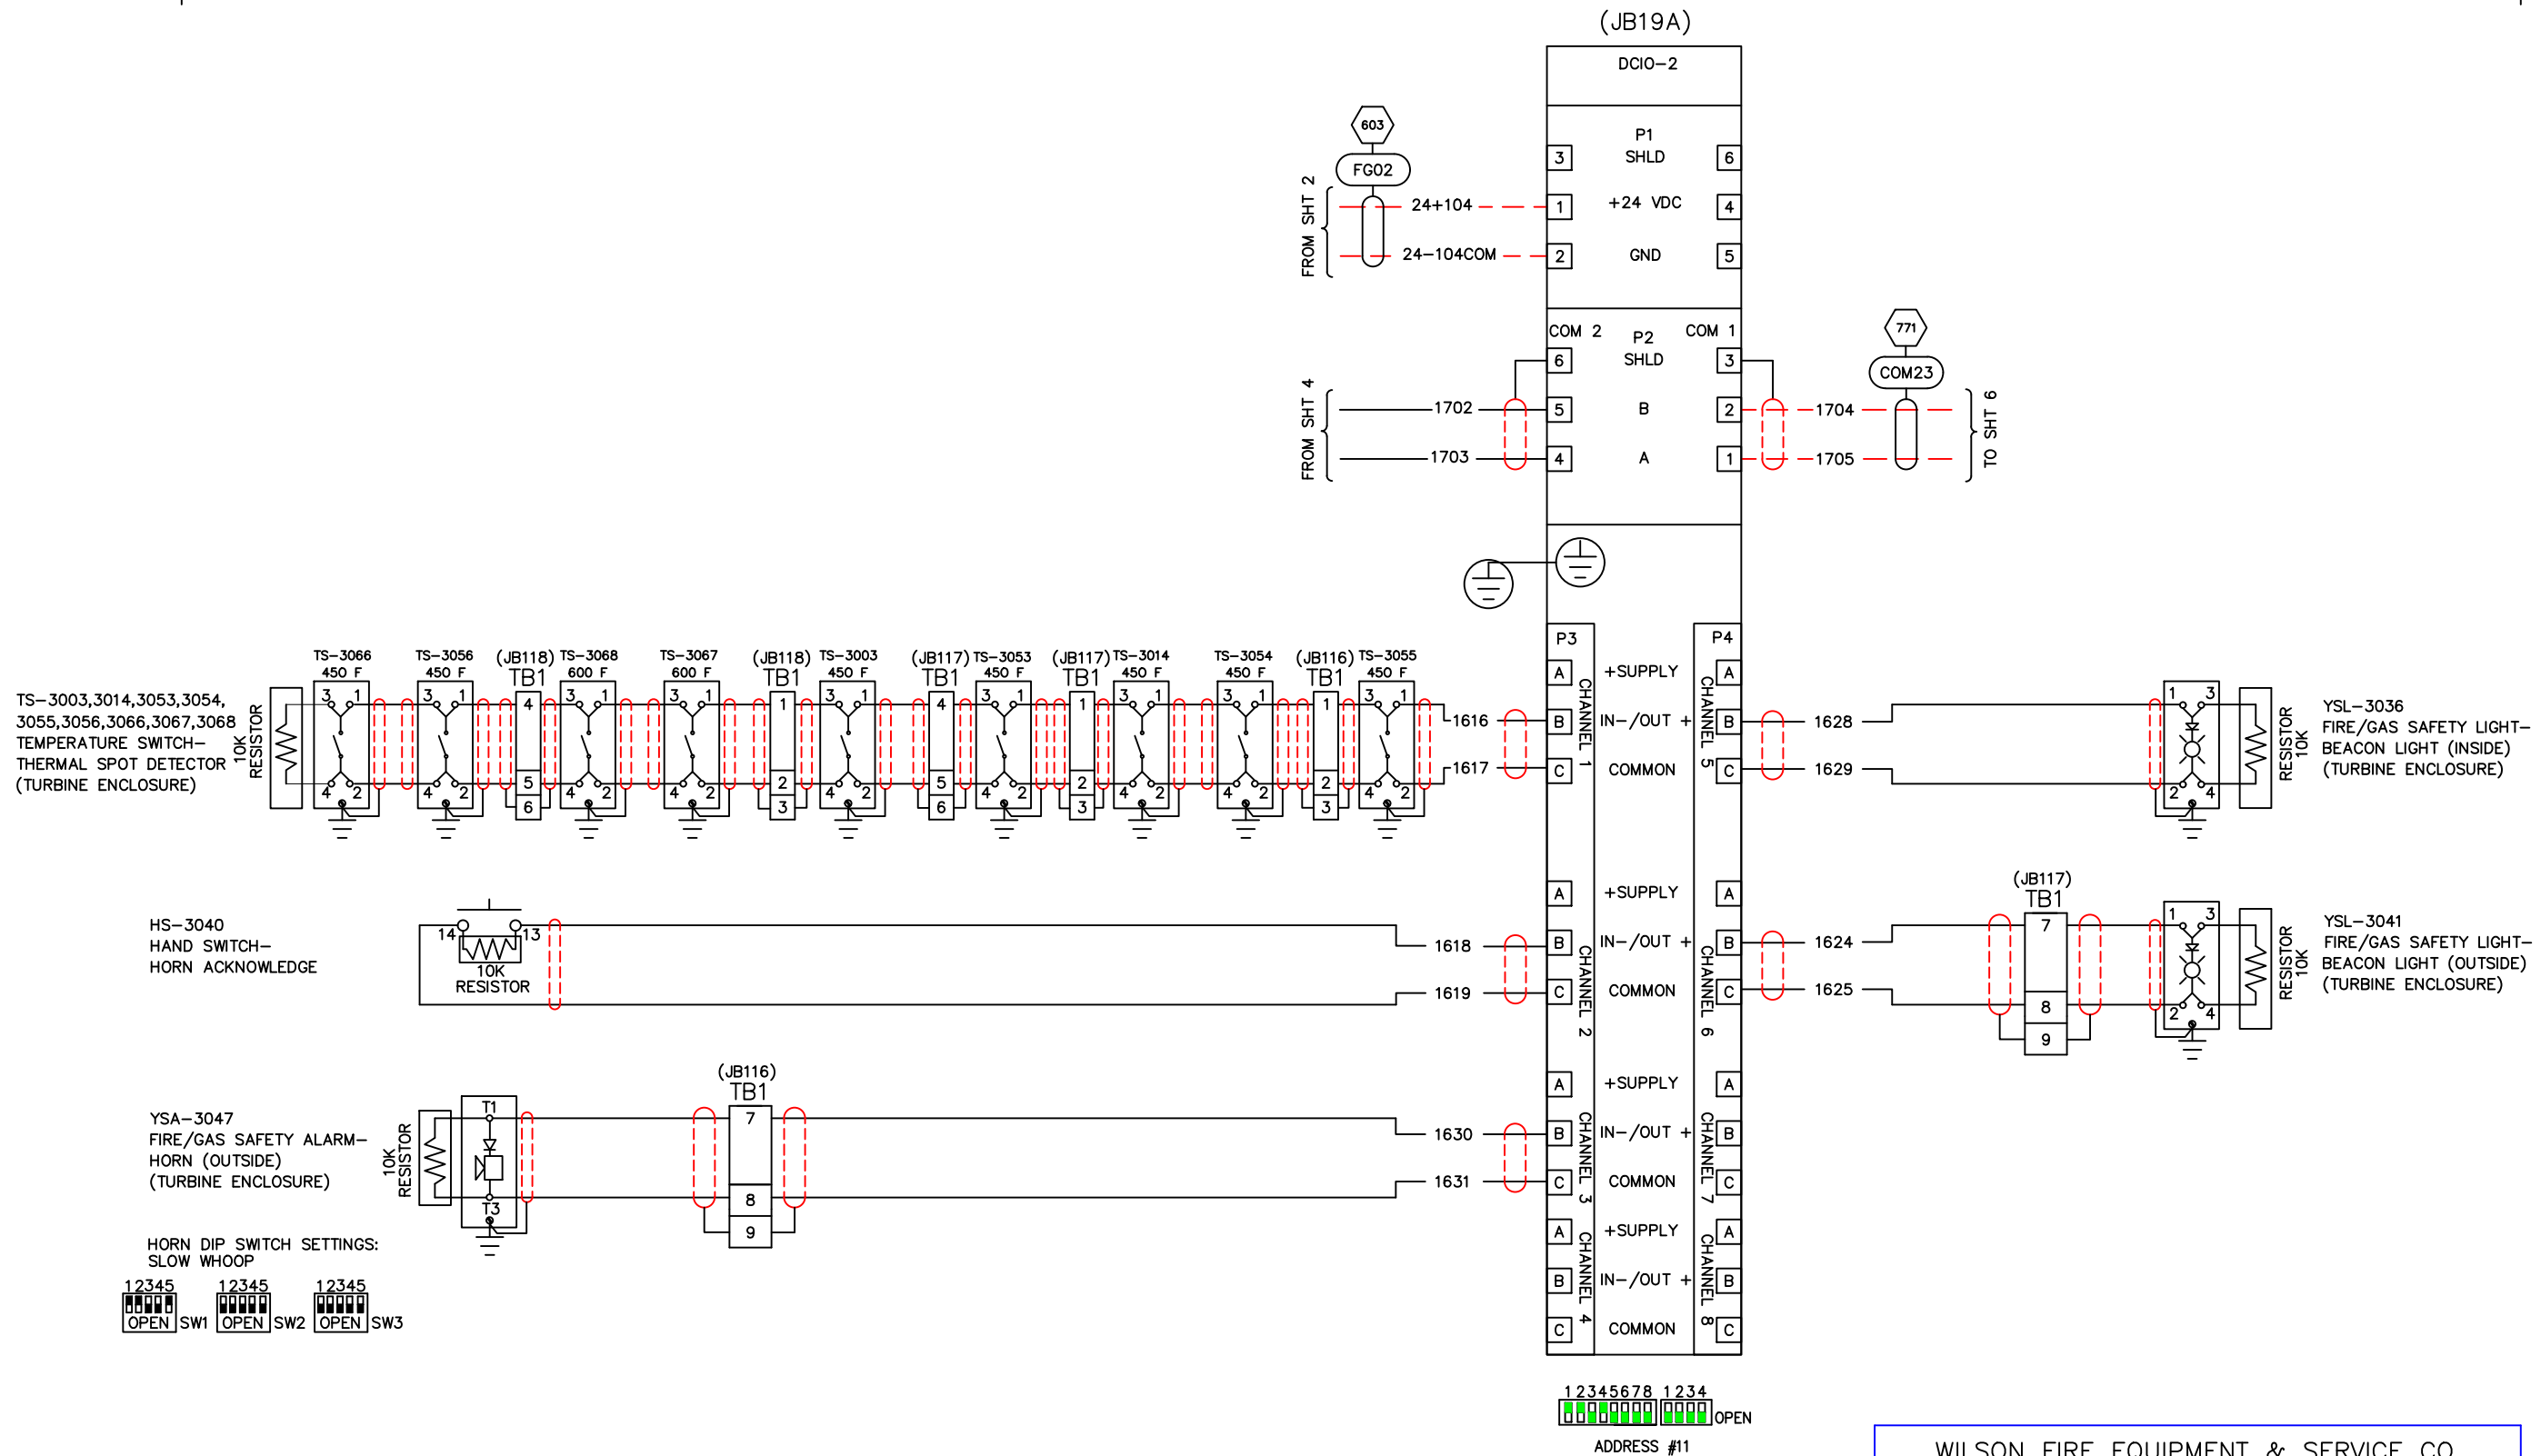

DRAWING SHEET APPLIES TO ALL UNITS

GE Mfg. No.	Hand	Unit No.
7264807	LH	2

REVISIONS			
REV	DESCRIPTION	DATE	BY
0	ISSUED FOR APPROVAL	01/07/16	MAP
1	REVISED PER CUSTOMER COMMENTS	02/05/16	MAP
2	REVISED PER CUSTOMER COMMENTS	07/11/16	JG
3	REVISED PER CUSTOMER COMMENTS	09/28/16	JG
4	REVISED PER CUSTOMER COMMENTS	11/17/16	JG
5	REVISED PER CUSTOMER COMMENTS	01/24/17	JG

THIS DRAWING, DESIGN AND THE DATA CONTAINED THEREIN IS THE PROPERTY OF WILSON FIRE EQUIPMENT AND IS NOT TO BE DISTRIBUTED TO OR USED BY OTHERS WITHOUT THE EXPRESSED WRITTEN CONSENT OF WILSON FIRE EQUIPMENT.


SCALE: AS SHOWN DATE: 01/07/16

DRAWN: MAP 01/07/16


CHECKED: LMW 01/24/17

APPROVED: LMW 01/24/17

WILSON FIRE EQUIPMENT & SERVICE CO. 7303 EMPIRE CENTRAL DRIVE HOUSTON, TEXAS 77040 (713) 896-4747		
CUSTOMER INFORMATION		
GE PACKAGED POWER LP. 7264807		
LMS100 60HZ EXELON PROJECT		
SYSTEM WIRING - DCIO-2 FIRE DETECTION / CO2 SUPPRESSION SYSTEM WFE PROJECT # GE-1378		

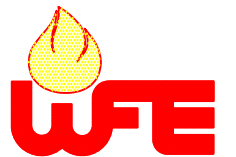

SIZE	DRAWING NO.	REV
B	SW-1378-05	5

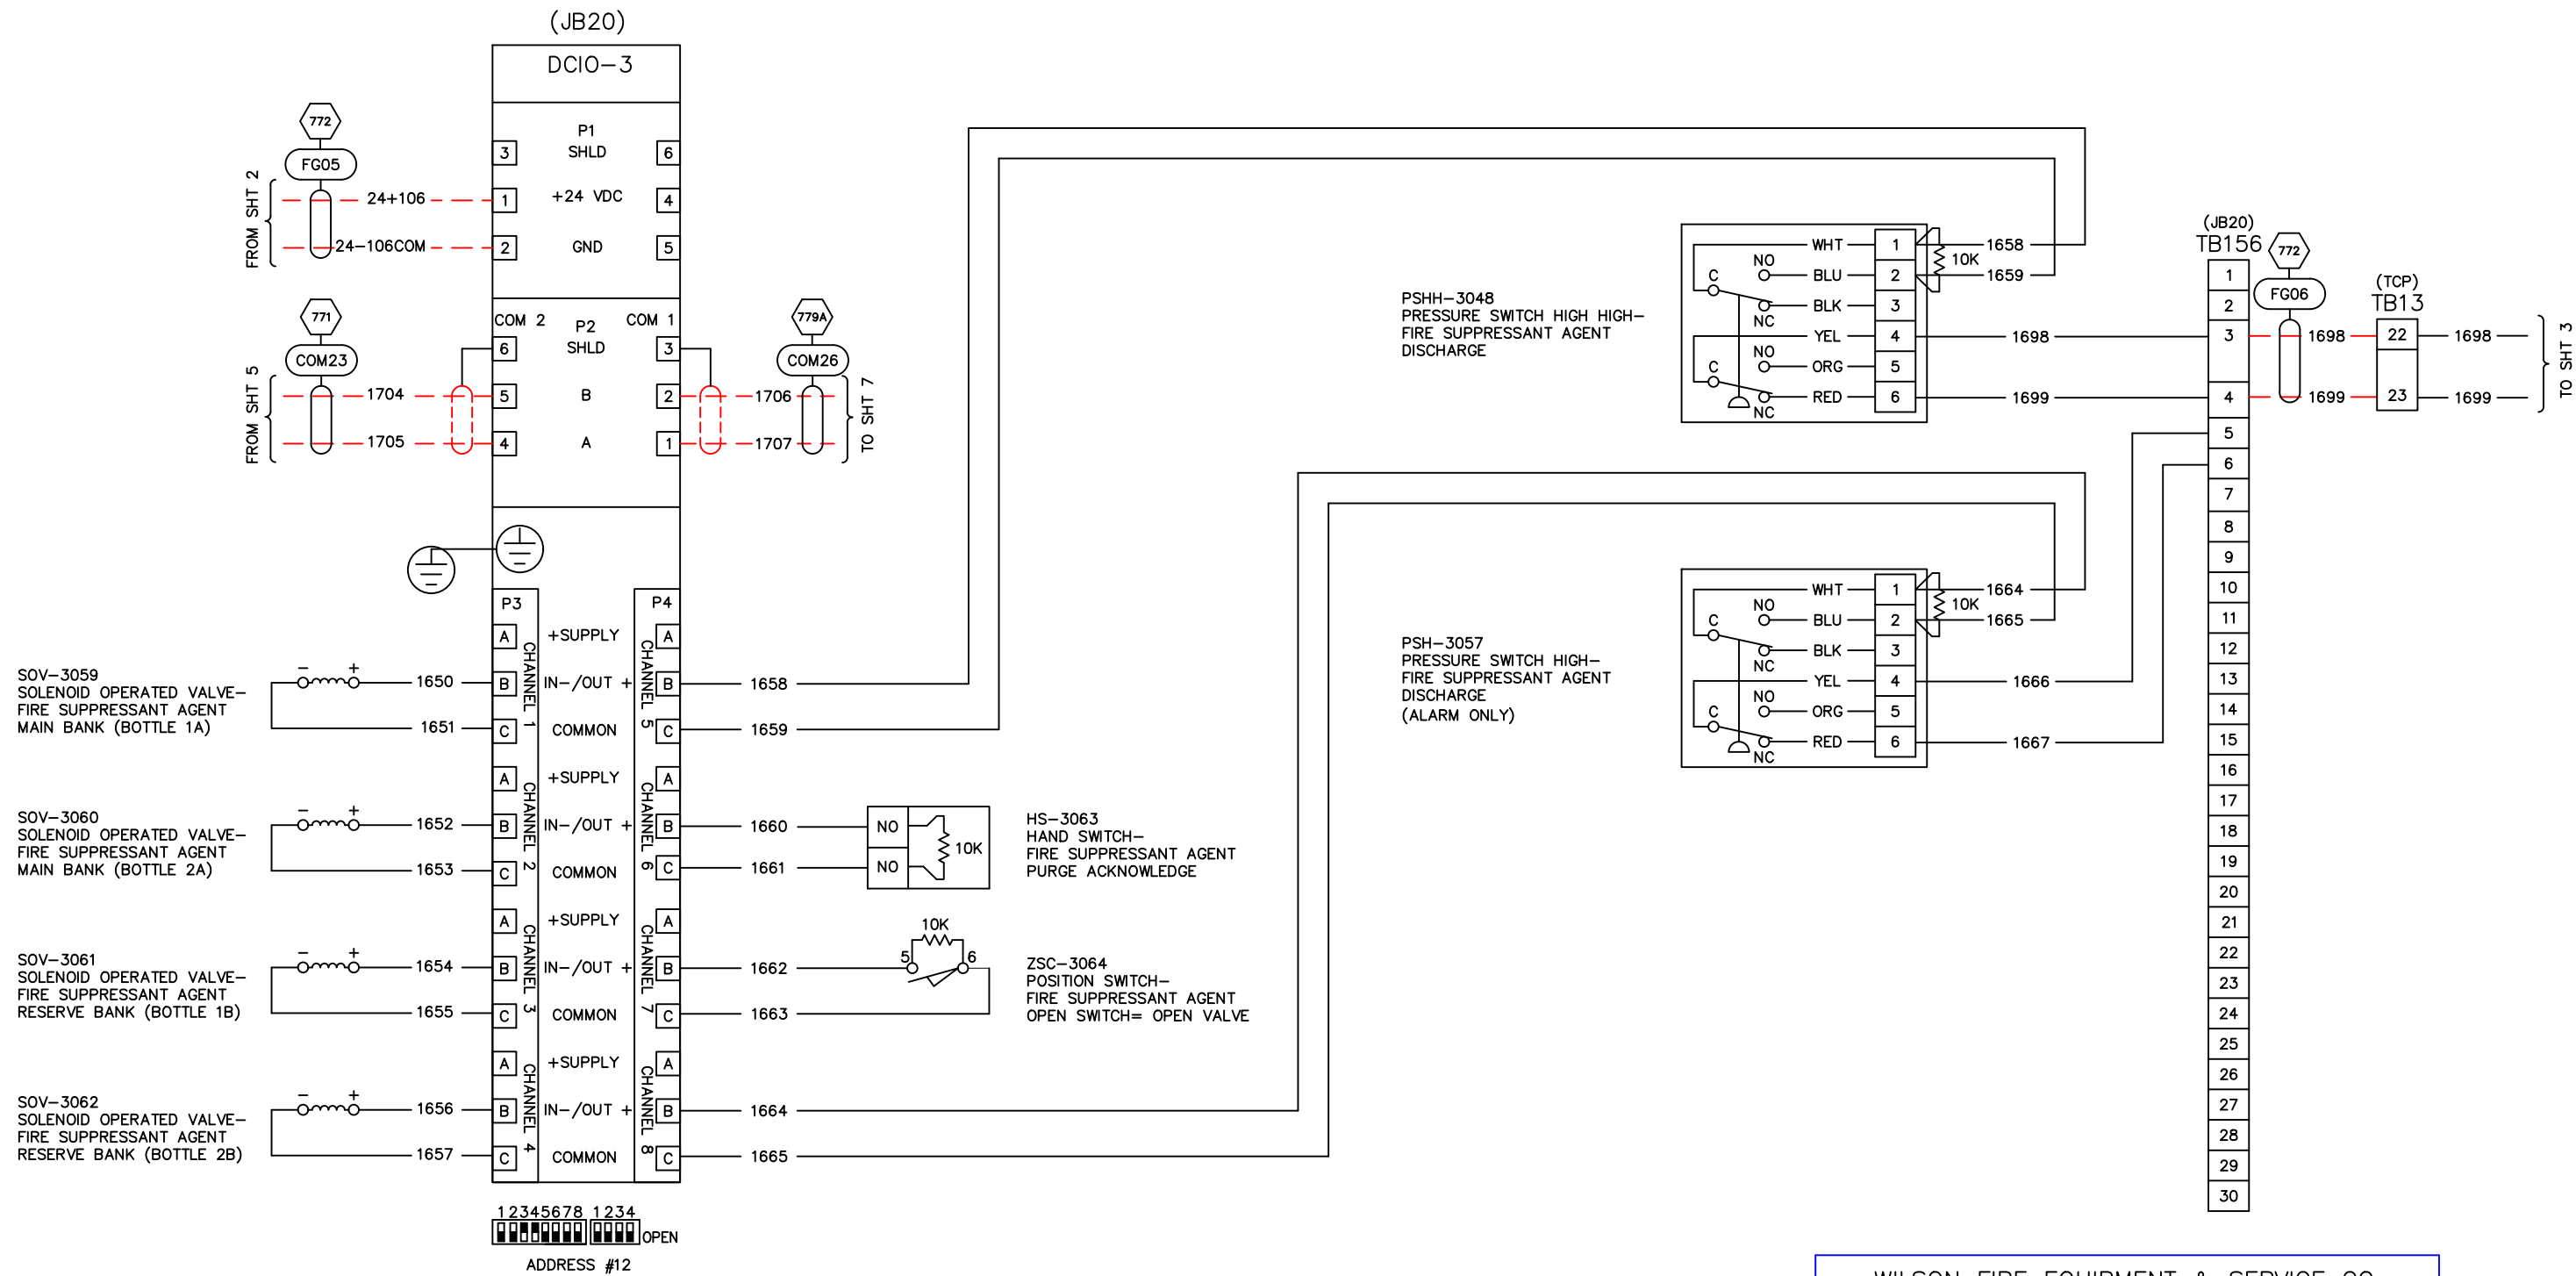

DRAWING SHEET APPLIES TO ALL UNITS


GE Mfg. No.	Hand	Unit No.
7264807	LH	2

REVISIONS				THIS DRAWING, DESIGN AND THE DATA CONTAINED THEREIN IS THE PROPERTY OF WILSON FIRE EQUIPMENT AND IS NOT TO BE DISTRIBUTED TO OR USED BY OTHERS WITHOUT THE EXPRESSED WRITTEN CONSENT OF WILSON FIRE EQUIPMENT.
REV	DESCRIPTION	DATE	BY	
0	ISSUED FOR APPROVAL	01/07/16	MAP	
1	REVISED PER CUSTOMER COMMENTS	02/05/16	MAP	
2	REVISED PER CUSTOMER COMMENTS	07/11/16	JG	
3	REVISED PER CUSTOMER COMMENTS	09/28/16	JG	
4	REVISED PER CUSTOMER COMMENTS	11/17/16	JG	
5	REVISED PER CUSTOMER COMMENTS	01/24/17	JG	
SCALE: AS SHOWN				DATE
DRAWN: MAP				01/07/16
CHECKED: LMW				01/24/17
APPROVED: LMW				01/24/17

WILSON FIRE EQUIPMENT & SERVICE CO. 7303 EMPIRE CENTRAL DRIVE HOUSTON, TEXAS 77040 (713) 896-4747		
CUSTOMER INFORMATION		
GE PACKAGED POWER LP. 7264807		
LMS100 60HZ EXELON PROJECT		
SYSTEM WIRING - DCIO-3 FIRE DETECTION / CO2 SUPPRESSION SYSTEM WFE PROJECT # GE-1378		



SIZE	DRAWING NO.	REV
B	SW-1378-06 SHEET 6 OF 15	5

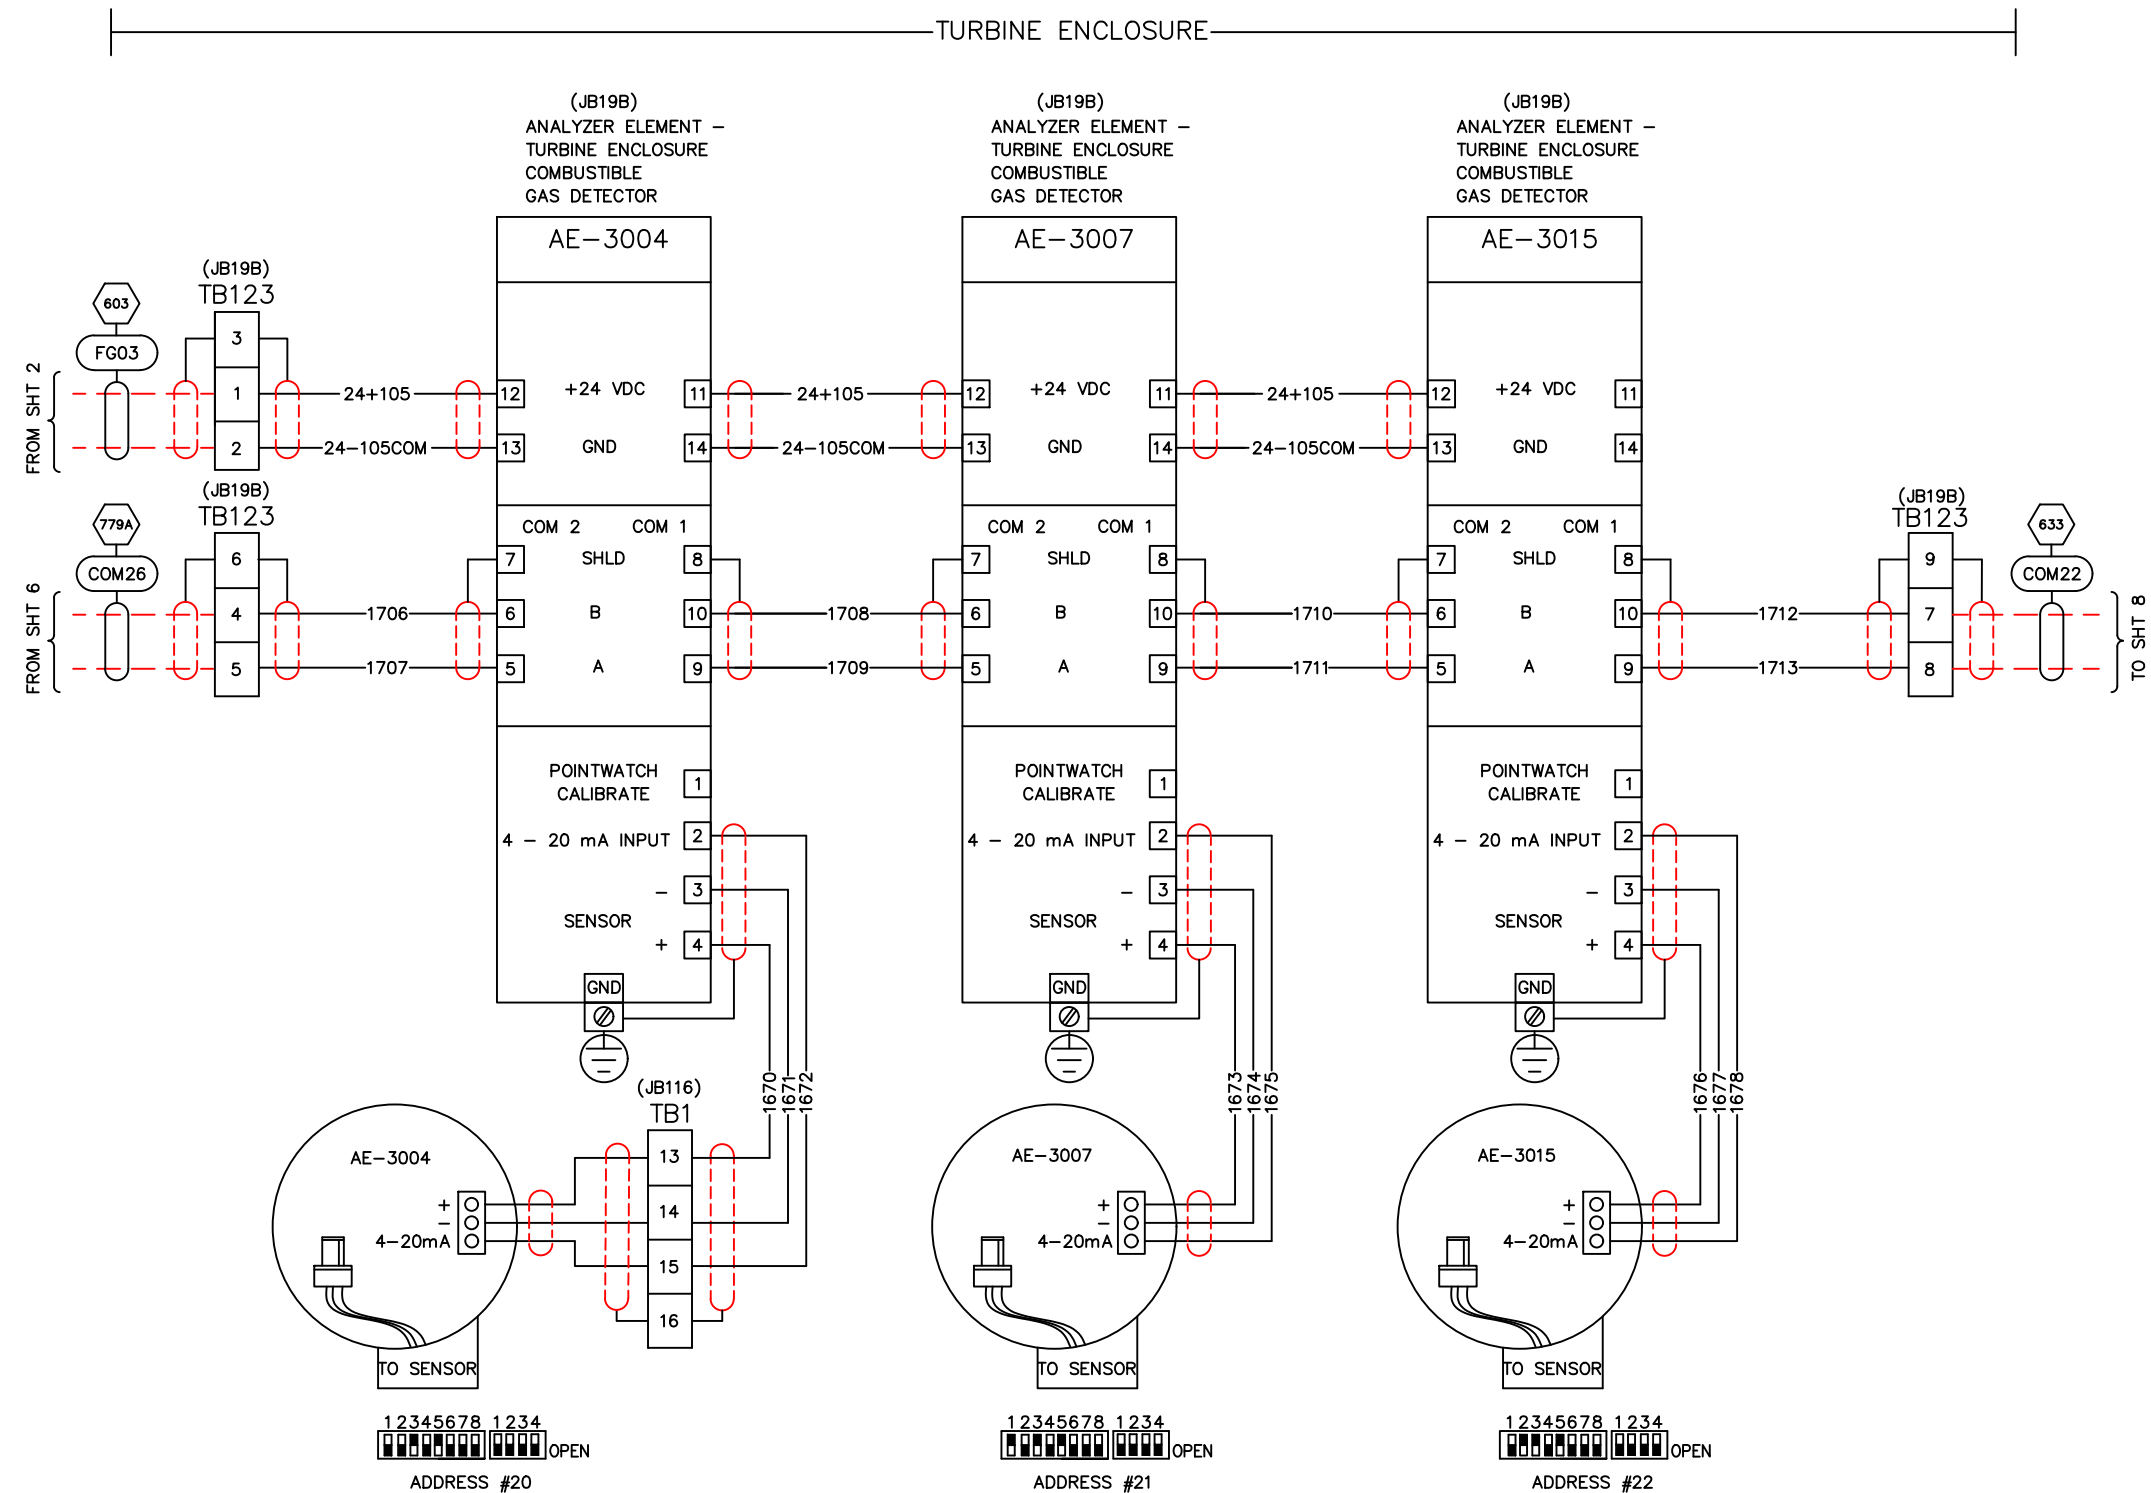

DRAWING SHEET APPLIES TO ALL UNITS

GE Mfg. No.	Hand	Unit No.
7264807	LH	2

REVISIONS			
REV	DESCRIPTION	DATE	BY
0	ISSUED FOR APPROVAL	01/07/16	MAP
1	REVISED PER CUSTOMER COMMENTS	02/05/16	MAP
2	REVISED PER CUSTOMER COMMENTS	07/11/16	JG
3	REVISED PER CUSTOMER COMMENTS	09/28/16	JG
4	REVISED PER CUSTOMER COMMENTS	11/17/16	JG
5	REVISED PER CUSTOMER COMMENTS	01/24/17	JG

THIS DRAWING, DESIGN AND THE DATA CONTAINED THEREIN IS THE PROPERTY OF WILSON FIRE EQUIPMENT AND IS NOT TO BE DISTRIBUTED TO OR USED BY OTHERS WITHOUT THE EXPRESSED WRITTEN CONSENT OF WILSON FIRE EQUIPMENT.

SCALE: AS SHOWN DATE: 01/07/16


DRAWN: MAP 01/07/16

CHECKED: LMW 01/24/17

APPROVED: LMW 01/24/17

WILSON FIRE EQUIPMENT & SERVICE CO. 7303 EMPIRE CENTRAL DRIVE HOUSTON, TEXAS 77040 (713) 896-4747	
CUSTOMER INFORMATION	
GE PACKAGED POWER LP. 7264807	
LMS100 60HZ EXELON PROJECT	
SYSTEM WIRING - INSTRUMENT LOOP DIAGRAM FIRE DETECTION / CO2 SUPPRESSION SYSTEM WFE PROJECT # GE-1378	

		
SIZE	DRAWING NO.	REV
B	SW-1378-07 SHEET 7 OF 15	5

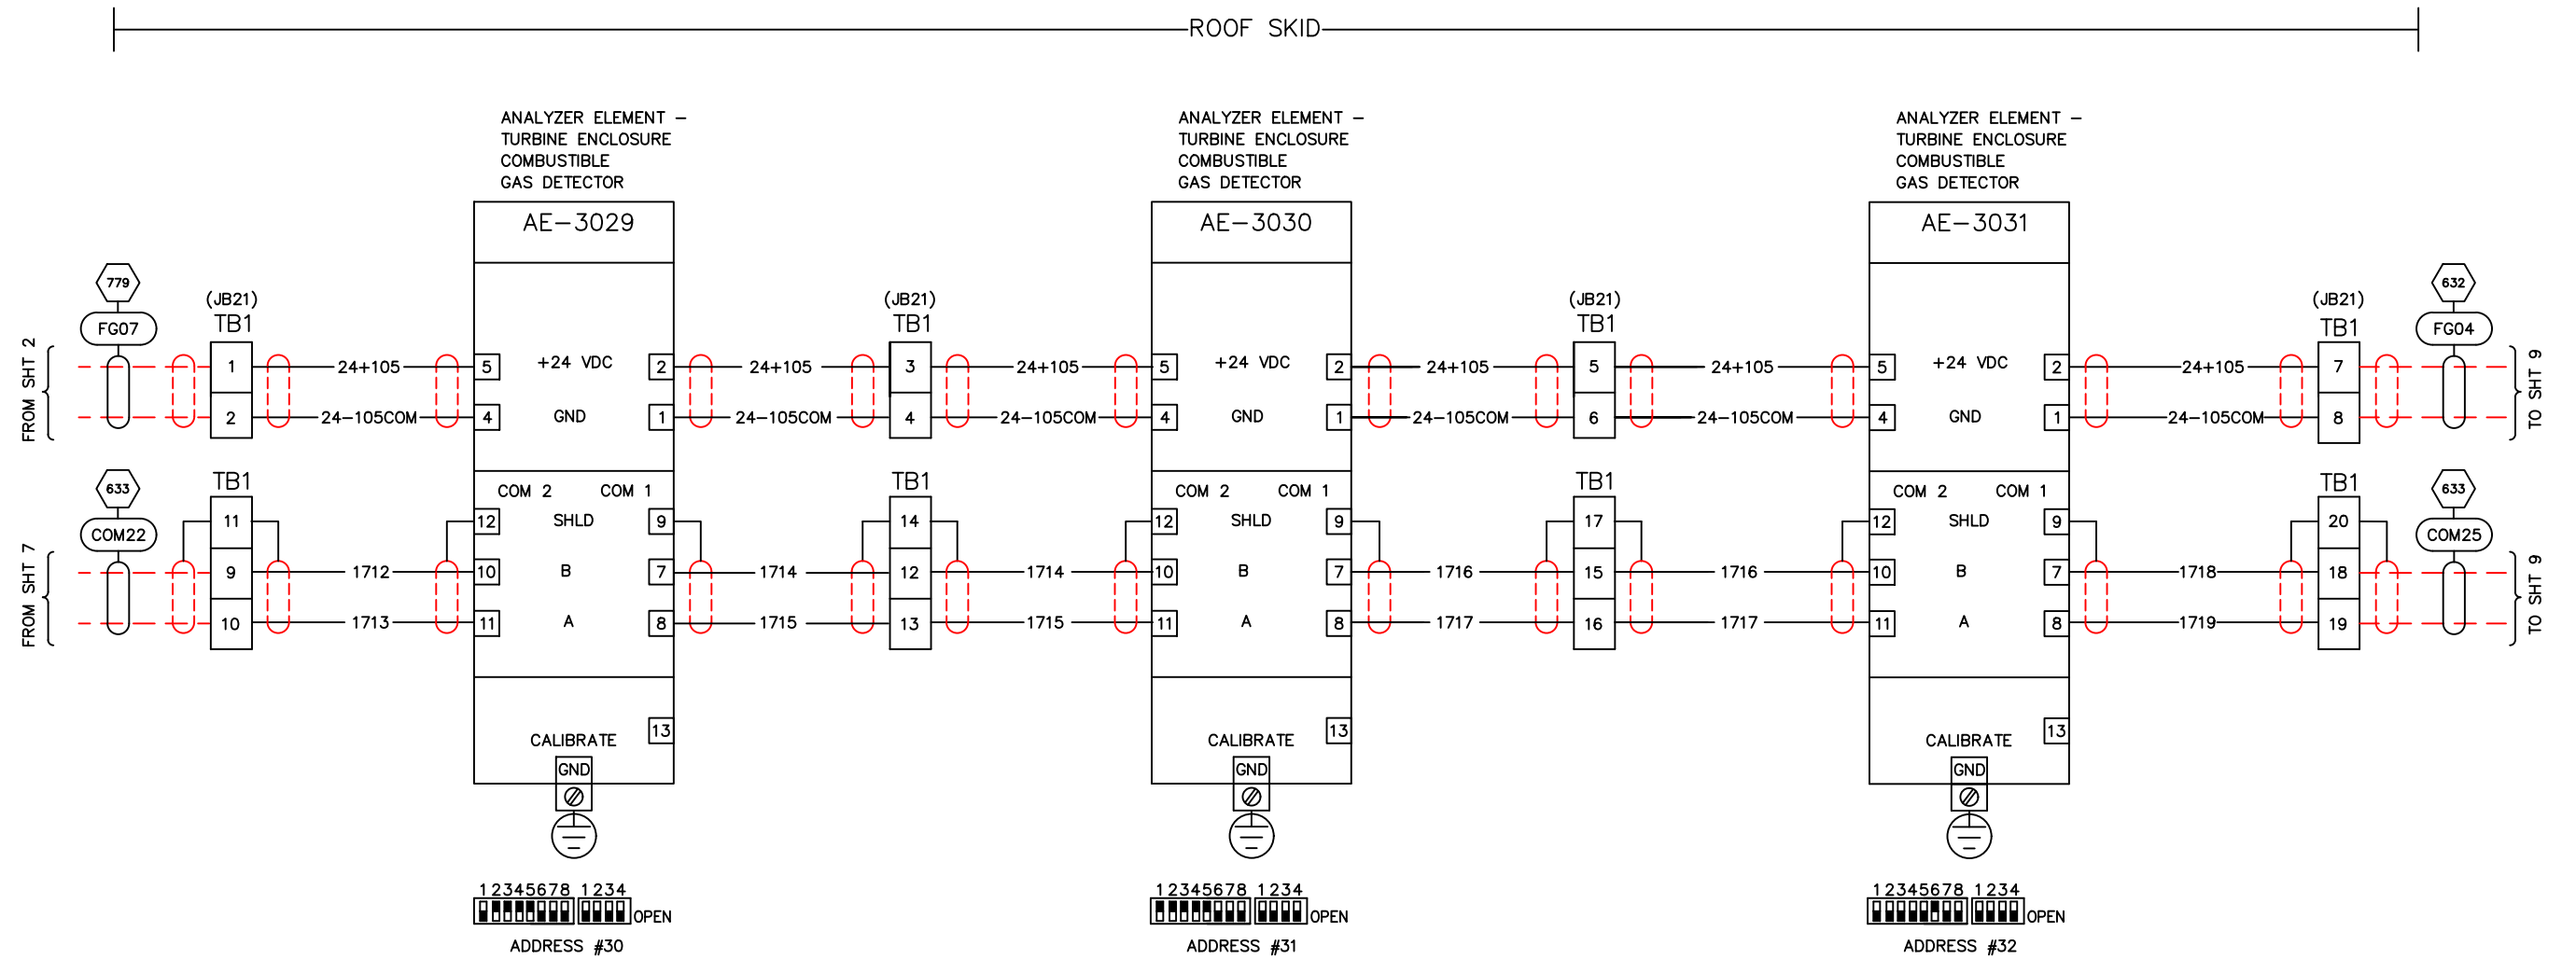

DRAWING SHEET APPLIES TO ALL UNITS

GE Mfg. No.	Hand	Unit No.
7264807	LH	2


REVISIONS			
REV	DESCRIPTION	DATE	BY
0	ISSUED FOR APPROVAL	01/07/16	MAP
1	REVISED PER CUSTOMER COMMENTS	02/05/16	MAP
2	REVISED PER CUSTOMER COMMENTS	07/11/16	JG
3	REVISED PER CUSTOMER COMMENTS	09/28/16	JG
4	REVISED PER CUSTOMER COMMENTS	11/17/16	JG
5	REVISED PER CUSTOMER COMMENTS	01/24/17	JG

THIS DRAWING, DESIGN AND THE DATA CONTAINED THEREIN IS THE PROPERTY OF WILSON FIRE EQUIPMENT AND IS NOT TO BE DISTRIBUTED TO OR USED BY OTHERS WITHOUT THE EXPRESSED WRITTEN CONSENT OF WILSON FIRE EQUIPMENT.

SCALE:	AS SHOWN	DATE
DRAWN:	MAP	01/07/16
CHECKED:	LMW	01/24/17
APPROVED:	LMW	01/24/17

WILSON FIRE EQUIPMENT & SERVICE CO. 7303 EMPIRE CENTRAL DRIVE HOUSTON, TEXAS 77040 (713) 896-4747	
CUSTOMER INFORMATION	
GE PACKAGED POWER LP. 7264807	
LMS100 60HZ EXELON PROJECT	
SYSTEM WIRING - INSTRUMENT LOOP DIAGRAM FIRE DETECTION / CO2 SUPPRESSION SYSTEM WFE PROJECT # GE-1378	

		
SIZE	DRAWING NO.	REV
B	SW-1378-08 SHEET 8 OF 15	5

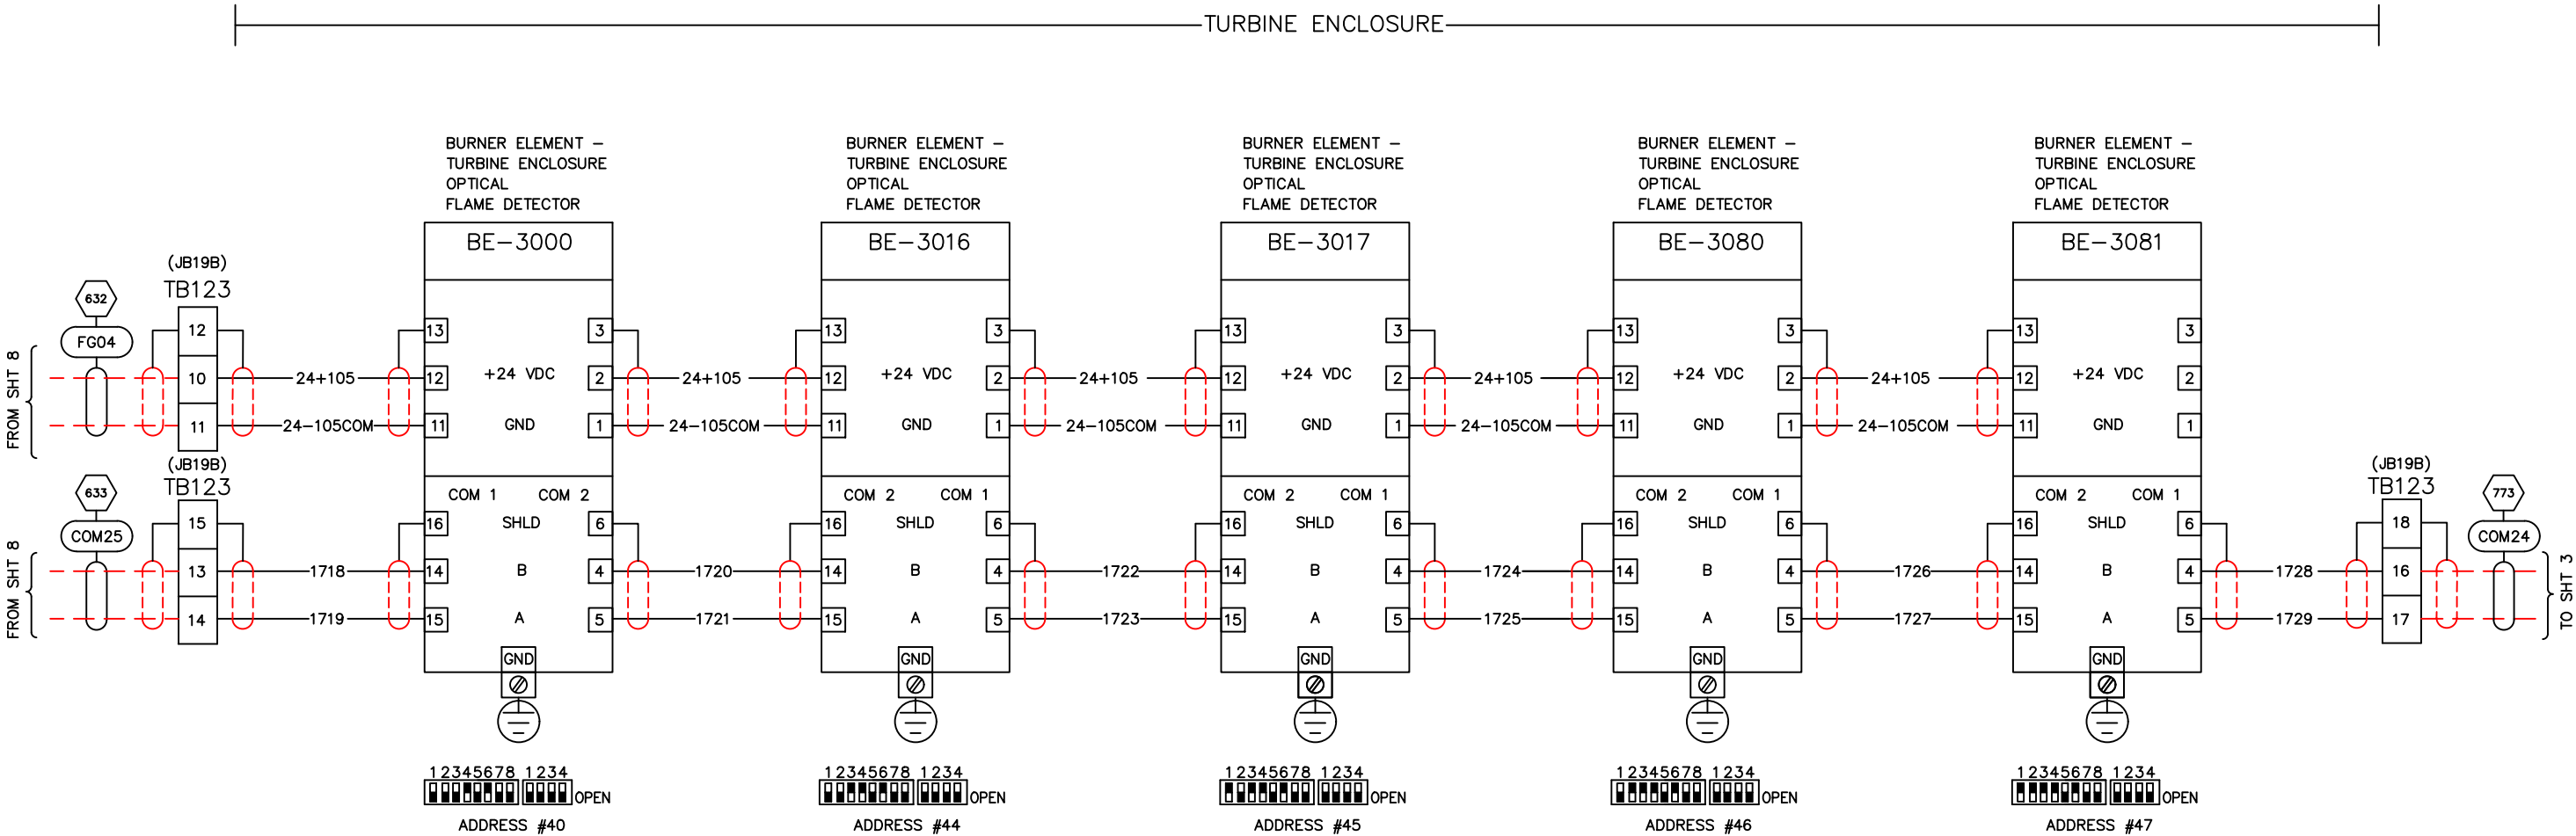

DRAWING SHEET APPLIES TO ALL UNITS

GE Mfg. No.	Hand	Unit No.
7264807	LH	2

REVISIONS				THIS DRAWING, DESIGN AND THE DATA CONTAINED THEREIN IS THE PROPERTY OF WILSON FIRE EQUIPMENT AND IS NOT TO BE DISTRIBUTED TO OR USED BY OTHERS WITHOUT THE EXPRESSED WRITTEN CONSENT OF WILSON FIRE EQUIPMENT.
REV	DESCRIPTION	DATE	BY	
0	ISSUED FOR APPROVAL	01/07/16	MAP	
1	REVISED PER CUSTOMER COMMENTS	02/05/16	MAP	
2	REVISED PER CUSTOMER COMMENTS	07/11/16	JG	
3	REVISED PER CUSTOMER COMMENTS	09/28/16	JG	
4	REVISED PER CUSTOMER COMMENTS	11/17/16	JG	
5	REVISED PER CUSTOMER COMMENTS	01/24/17	JG	
				SCALE: AS SHOWN DATE
				DRAWN: MAP 01/07/16
				CHECKED: LMW 01/24/17
				APPROVED: LMW 01/24/17

WILSON FIRE EQUIPMENT & SERVICE CO. 7303 EMPIRE CENTRAL DRIVE HOUSTON, TEXAS 77040 (713) 896-4747	
CUSTOMER INFORMATION	
GE PACKAGED POWER LP. 7264807	
LMS100 60HZ EXELON PROJECT	
SYSTEM WIRING - INSTRUMENT LOOP DIAGRAM FIRE DETECTION / CO2 SUPPRESSION SYSTEM WFE PROJECT # GE-1378	

		
SIZE	DRAWING NO.	REV
B	SW-1378-09 SHEET 9 OF 15	5

Node Add	Device Type	Tag Name	Description	Node Configuration Settings															
1	CONTROLLER			Config Port Baud Rate: 115200	Parity: NONE	Serial Port Protocol: MODBUS SLAVE	MODBUS Baud Rate: 115200		Parity: NONE	Beeper Volume: HIGH	Allow Lon Point Disabling: YES	Option Board:	Control Net:	Control Net Mac Address: 17					
	CONTROLLER INPUTS			INTPUT 1: NONE	INTPUT 2: NONE	INTPUT 3: NONE	INTPUT 4: NONE		INTPUT 5: NONE	INTPUT 6: NONE	INTPUT 7: NONE	INTPUT 8: NONE							
	CONTROLLER OUTPUTS			OUTPUT 1:	OUTPUT 2:	OUTPUT 3:	OUTPUT4:		OUTPUT 5:	OUTPUT 6	OUTPUT 7:	OUTPUT 8: NONE							
	RELAY-1		FIRE/GAS MONITOR SHUTDOWN																
	RELAY-2																		
	RELAY-3		ALARM LEL-TURBINE ROOM																
	RELAY-4		RELAY FAULT (CUSTOMER)																
	RELAY-5		SHUTDOWN LEL-TURBINE ROOM																
	RELAY-6		F&G SUPPRESSANT AGENT RELEASE (CUSTOMER)																
	RELAY-7		CRITICAL PATH SHUTDOWN																
	RELAY-8		GENERAL ALARM (CUSTOMER)																
Node Add	Device Type	Tag Name	Description	Node Configuration Settings															
10	DCIO1							123456781234 OPEN											
	DCIO1 CH 1	JB19A-1-1	HS-3070 THRU 3077 MANUAL CO2 RELEASE STATION	CHANNEL TYPE: INPUT	SUPERVISION: OPENS	STATIC LOGIC MODE (INPUT):	FIRE ALARM	30 SEC.											
	DCIO1 CH 2	JB19A-1-2	YSA-3046, FIRE/GAS SAFETY ALARM HORN (INSIDE) (TURBINE ENCLOSURE)	CHANNEL TYPE: OUTPUT	SUPERVISION: OPENS			ACTIVATION TIME (OUTPUT): 0											
	DCIO1 CH 3	JB19A-1-3	YSL-3043 FIRE/GAS SAFETY LIGHT BEACON (INSIDE) (TURBINE ENCLOSURE)	CHANNEL TYPE: OUTPUT	SUPERVISION: OPENS			ACTIVATION TIME (OUTPUT): 0											
	DCIO1 CH 4	JB19A-1-4																	
	DCIO1 CH 5	JB19A-1-5	YSL-3042 FIRE/GAS SAFETY LIGHT BEACON (OUTSIDE) (TURBINE ENCLOSURE)	CHANNEL TYPE: OUTPUT	SUPERVISION: OPENS			ACTIVATION TIME (OUTPUT): 0											
	DCIO1 CH 6	JB19A-1-6	YSA-3006, FIRE/GAS SAFETY ALARM HORN (OUTSIDE) (TURBINE ENCLOSURE)	CHANNEL TYPE: INPUT	SUPERVISION: OPENS	STATIC LOGIC MODE (INPUT):	FIRE ALARM	30 SEC.											
	DCIO1 CH 7	JB19A-1-7		CHANNEL TYPE: INPUT	SUPERVISION: NONE	STATIC LOGIC MODE (INPUT):		0											
	DCIO1 CH 8	JB19A-1-8		CHANNEL TYPE: INPUT	SUPERVISION: NONE	STATIC LOGIC MODE (INPUT):		0											
Node Add	Device Type	Tag Name	Description	Node Configuration Settings															
11	DCIO2							123456781234 OPEN											
	DCIO2 CH 1	JB19A-2-1	TS-3003, 3014, 3053 THRU 3056, 3066, 3067, 3068 THERMAL SPOT DETECTOR (TURBINE)	CHANNEL TYPE: INPUT	SUPERVISION: OPENS	STATIC LOGIC MODE (INPUT):	FIRE ALARM	30 SEC.											
	DCIO2 CH 2	JB19A-2-2	HS-3040 HORN ACKNOWLEDGE (TURBINE ENCLOSURE)	CHANNEL TYPE: INPUT	SUPERVISION: NONE	STATIC LOGIC MODE (INPUT):	FIRE ALARM	0											
	DCIO2 CH 3	JB19A-2-3	YSA-3047, FIRE/GAS SAFETY ALARM HORN (OUTSIDE) (TURBINE ENCLOSURE)	CHANNEL TYPE: OUTPUT	SUPERVISION: OPENS			ACTIVATION TIME (OUTPUT): 0											
	DCIO2 CH 4	JB19A-2-4																	
	DCIO2 CH 5	JB19A-2-5	YSL-3036 FIRE/GAS SAFETY ALARM BEACON (INSIDE) (TURBINE ENCLOSURE)	CHANNEL TYPE: OUTPUT	SUPERVISION: OPENS			ACTIVATION TIME (OUTPUT): 0											
	DCIO2 CH 6	JB19A-2-6	YSL-3041 FIRE/GAS SAFETY LIGHT BEACON (OUTSIDE) (TURBINE ENCLOSURE)	CHANNEL TYPE: OUTPUT	SUPERVISION: OPENS			ACTIVATION TIME (OUTPUT): 0											
	DCIO2 CH 7	JB19A-2-7		CHANNEL TYPE: OUTPUT	SUPERVISION: OPENS			ACTIVATION TIME (OUTPUT): 0											
	DCIO2 CH 8	JB19A-2-8		CHANNEL TYPE: INPUT	SUPERVISION: NONE			ACTIVATION TIME (OUTPUT): 0											

DRAWING SHEET APPLIES TO ALL UNITS

GE Mfg. No.	Hand	Unit No.
7264807	LH	2

REVISIONS				THIS DRAWING, DESIGN AND THE DATA CONTAINED THEREIN IS THE PROPERTY OF WILSON FIRE EQUIPMENT AND IS NOT TO BE DISTRIBUTED TO OR USED BY OTHERS WITHOUT THE EXPRESSED WRITTEN CONSENT OF WILSON FIRE EQUIPMENT. SCALE: AS SHOWN DATE DRAWN: MAP 01/07/16 CHECKED: LMW 01/24/17 APPROVED: LMW 01/24/17	
REV	DESCRIPTION	DATE	BY		
0	ISSUED FOR APPROVAL	01/07/16	MAP		
1	REVISED PER CUSTOMER COMMENTS	02/05/16	MAP		
2	REVISED PER CUSTOMER COMMENTS	07/11/16	JG		
3	REVISED PER CUSTOMER COMMENTS	09/28/16	JG		
4	REVISED PER CUSTOMER COMMENTS	11/17/16	JG		
5	REVISED PER CUSTOMER COMMENTS	01/24/17	JG		

WILSON FIRE EQUIPMENT & SERVICE CO. 7303 EMPIRE CENTRAL DRIVE HOUSTON, TEXAS 77040 (713) 896-4747	
CUSTOMER INFORMATION	
GE PACKAGED POWER LP. 7264807	
LMS100 60HZ EXELON PROJECT	
SYSTEM WIRING – LON LIST FIRE DETECTION / CO2 SUPPRESSION SYSTEM WFE PROJECT # GE-1378	

		
SIZE	DRAWING NO.	REV
B	SW-1378-10 SHEET 10 OF 15	5

NODE ADD	DEVICE TYPE	TAG NAME	DESCRIPTION	NODE CONFIGURATION SETTINGS												
12	DCIO										12345678 00000000 1234 0000 OPEN					
	DCIO CH 1	JB20-1	SOV-3059 SOLENOID OPERATED VALVE MAIN BANK BOTTLE 1A	CHANNEL TYPE: OUTPUT	SUPERVISION: OPEN		ACTIVATION TIME (OUTPUT): 30 SEC									
	DCIO CH 2	JB20-2	SOV-3060 SOLENOID OPERATED VALVE MAIN BANK BOTTLE 2A	CHANNEL TYPE: OUTPUT	SUPERVISION: OPEN		ACTIVATION TIME (OUTPUT): 30 SEC									
	DCIO CH 3	JB20-3	SOV-3061 SOLENOID OPERATED VALVE RESERVE BANK BOTTLE 1B	CHANNEL TYPE: OUTPUT	SUPERVISION: OPEN		ACTIVATION TIME (OUTPUT): 30 SEC									
	DCIO CH 4	JB20-4	SOV-3062 SOLENOID OPERATED VALVE RESERVE BANK BOTTLE 2B	CHANNEL TYPE: OUTPUT	SUPERVISION: OPEN		ACTIVATION TIME (OUTPUT): 30 SEC									
	DCIO CH 5	JB20-5	PSHH-3048 PRESSURE SWITCH HI HI CO2 DISCHARGE	CHANNEL TYPE: INPUT	SUPERVISION: OPEN	STATIC LOGIC FIRE MODE (INPUT): ALARM		ACTIVATION TIME 5 SEC. W/O PRESSURE SWITCH (OUTPUT): 90 SEC. W/ PRESSURE SWITCH								
	DCIO CH 6	JB20-6	HS-3063 HANDSWITCH PURGE ACKNOWLEDGE CO2	CHANNEL TYPE: INPUT	SUPERVISION: OPEN	STATIC LOGIC FIRE MODE (INPUT): ALARM		0								
	DCIO CH 7	JB20-7	ZSC-3064 POSITION SWITCH BLOCK VALVE CO2	CHANNEL TYPE: INPUT	SUPERVISION: OPEN	STATIC LOGIC INHIBIT MODE (INPUT): CO2 SYSTEM		0								
	DCIO CH 8	JB20-8	PSH-3057 PRESSURE SWITCH HIGH CO2 ALARM ONLY	CHANNEL TYPE: INPUT	SUPERVISION: OPEN	STATIC LOGIC FIRE MODE (INPUT): ALARM										
NODE ADD	DEVICE TYPE	TAG NAME	DESCRIPTION	NODE CONFIGURATION SETTINGS												
20	DCU	AE-3004	AE-3004 ANALYZER ELEMENT COMBUSTIBLE GAS DETECTOR	DCU TYPE: EXPLOSIVE	HIGH ALARM: 25	LOW ALARM: 15	CAL LEVEL: 50	GAS MODE: GAS DETECTOR			12345678 00000000 1234 0000 OPEN					DEADBAND 5
21	DCU	AE-3007	AE-3007 ANALYZER ELEMENT COMBUSTIBLE GAS DETECTOR	DCU TYPE: EXPLOSIVE	HIGH ALARM: 25	LOW ALARM: 15	CAL LEVEL: 50	GAS MODE: GAS DETECTOR			12345678 00000000 1234 0000 OPEN					DEADBAND 5
22	DCU	AE-3015	AE-3015 ANALYZER ELEMENT COMBUSTIBLE GAS DETECTOR	DCU TYPE: EXPLOSIVE	HIGH ALARM: 25	LOW ALARM: 15	CAL LEVEL: 50	GAS MODE: GAS DETECTOR			12345678 00000000 1234 0000 OPEN					DEADBAND 5
30	ECLIPSE	AE-3029	AE-3029 ANALYZER ELEMENT IR GAS DETECTOR	GAS TYPE: METHANE	CAL GAS TYPE: SAME	CAL METHOD: STD	UNITS: %LEL	HIGH ALARM: 10	LOW ALARM: 5	12345678 00000000 1234 0000 OPEN	CAL LEVEL: 50	LOW ALARM: NON-LATCHING:	HIGH ALARM: LATCHING	DEADBAND 5		
31	ECLIPSE	AE-3030	AE-3030 ANALYZER ELEMENT IR GAS DETECTOR	GAS TYPE: METHANE	CAL GAS TYPE: SAME	CAL METHOD: STD	UNITS: %LEL	HIGH ALARM: 10	LOW ALARM: 5	12345678 00000000 1234 0000 OPEN	CAL LEVEL: 50	LOW ALARM: NON-LATCHING:	HIGH ALARM: LATCHING	DEADBAND 5		
32	ECLIPSE	AE-3031	AE-3031 ANALYZER ELEMENT IR GAS DETECTOR	GAS TYPE: METHANE	CAL GAS TYPE: SAME	CAL METHOD: STD	UNITS: %LEL	HIGH ALARM: 10	LOW ALARM: 5	12345678 00000000 1234 0000 OPEN	CAL LEVEL: 50	LOW ALARM: NON-LATCHING:	HIGH ALARM: LATCHING	DEADBAND 5		
40	X9800 IR	BE-3000	BE-3000 BURNER ELEMENT SFIR OPTICAL FLAME DETECTOR TURBINE ROOM	NON-LATCHING:	TIME DELAY: 0		Oi MODE: AUTO	HEATER: ENABLED	IR SENS: MEDIUM	12345678 00000000 1234 0000 OPEN	PROCESSING MODE (IR): TDSA	IR Oi TEST FREQ: 1	FAILED IR Oi TEST FOR FAULT: 1	DEADBAND 5		
44	X9800 IR	BE-3016	BE-3016 BURNER ELEMENT SFIR OPTICAL FLAME DETECTOR TURBINE ROOM	NON-LATCHING:	TIME DELAY: 0		Oi MODE: AUTO	HEATER: ENABLED	IR SENS: MEDIUM	12345678 00000000 1234 0000 OPEN	PROCESSING MODE (IR): TDSA	IR Oi TEST FREQ: 1	FAILED IR Oi TEST FOR FAULT: 1	DEADBAND 5		
45	X9800 IR	BE-3017	BE-3017 BURNER ELEMENT SFIR OPTICAL FLAME DETECTOR TURBINE ROOM	NON-LATCHING:	TIME DELAY: 0		Oi MODE: AUTO	HEATER: ENABLED	IR SENS: MEDIUM	12345678 00000000 1234 0000 OPEN	PROCESSING MODE (IR): TDSA	IR Oi TEST FREQ: 1	FAILED IR Oi TEST FOR FAULT: 1	DEADBAND 5		
46	X9800 IR	BE-3080	BE-3080 BURNER ELEMENT SFIR OPTICAL FLAME DETECTOR TURBINE ROOM	NON-LATCHING:	TIME DELAY: 0		Oi MODE: AUTO	HEATER: ENABLED	IR SENS: MEDIUM	12345678 00000000 1234 0000 OPEN	PROCESSING MODE (IR): TDSA	IR Oi TEST FREQ: 1	FAILED IR Oi TEST FOR FAULT: 1	DEADBAND 5		
47	X9800 IR	BE-3081	BE-3081 BURNER ELEMENT SFIR OPTICAL FLAME DETECTOR TURBINE ROOM	NON-LATCHING:	TIME DELAY: 0		Oi MODE: AUTO	HEATER: ENABLED	IR SENS: MEDIUM	12345678 00000000 1234 0000 OPEN	PROCESSING MODE (IR): TDSA	IR Oi TEST FREQ: 1	FAILED IR Oi TEST FOR FAULT: 1	DEADBAND 5		

DRAWING SHEET APPLIES TO ALL UNITS

GE Mfg. No.	Hand	Unit No.
7264807	LH	2

REVISIONS				THIS DRAWING, DESIGN AND THE DATA CONTAINED THEREIN IS THE PROPERTY OF WILSON FIRE EQUIPMENT AND IS NOT TO BE DISTRIBUTED TO OR USED BY OTHERS WITHOUT THE EXPRESSED WRITTEN CONSENT OF WILSON FIRE EQUIPMENT.
REV	DESCRIPTION	DATE	BY	
0	ISSUED FOR APPROVAL	01/07/16	MAP	
1	REVISED PER CUSTOMER COMMENTS	02/05/16	MAP	
2	REVISED PER CUSTOMER COMMENTS	07/11/16	JG	
3	REVISED PER CUSTOMER COMMENTS	09/28/16	JG	
4	REVISED PER CUSTOMER COMMENTS	11/17/16	JG	
5	REVISED PER CUSTOMER COMMENTS	01/24/17	JG	
SCALE: AS SHOWN				DATE
DRAWN: MAP				01/07/16
CHECKED: LMW				01/24/17
APPROVED: LMW				01/24/17

WILSON FIRE EQUIPMENT & SERVICE CO. 7303 EMPIRE CENTRAL DRIVE HOUSTON, TEXAS 77040 (713) 896-4747		
CUSTOMER INFORMATION		
GE PACKAGED POWER LP. 7264807		
LMS100 60HZ EXELON PROJECT		
SYSTEM WIRING – LON LIST FIRE DETECTION / CO2 SUPPRESSION SYSTEM WFE PROJECT # GE-1378		

WFE		
SIZE	DRAWING NO.	REV
B	SW-1378-11 SHEET 11 OF 15	5